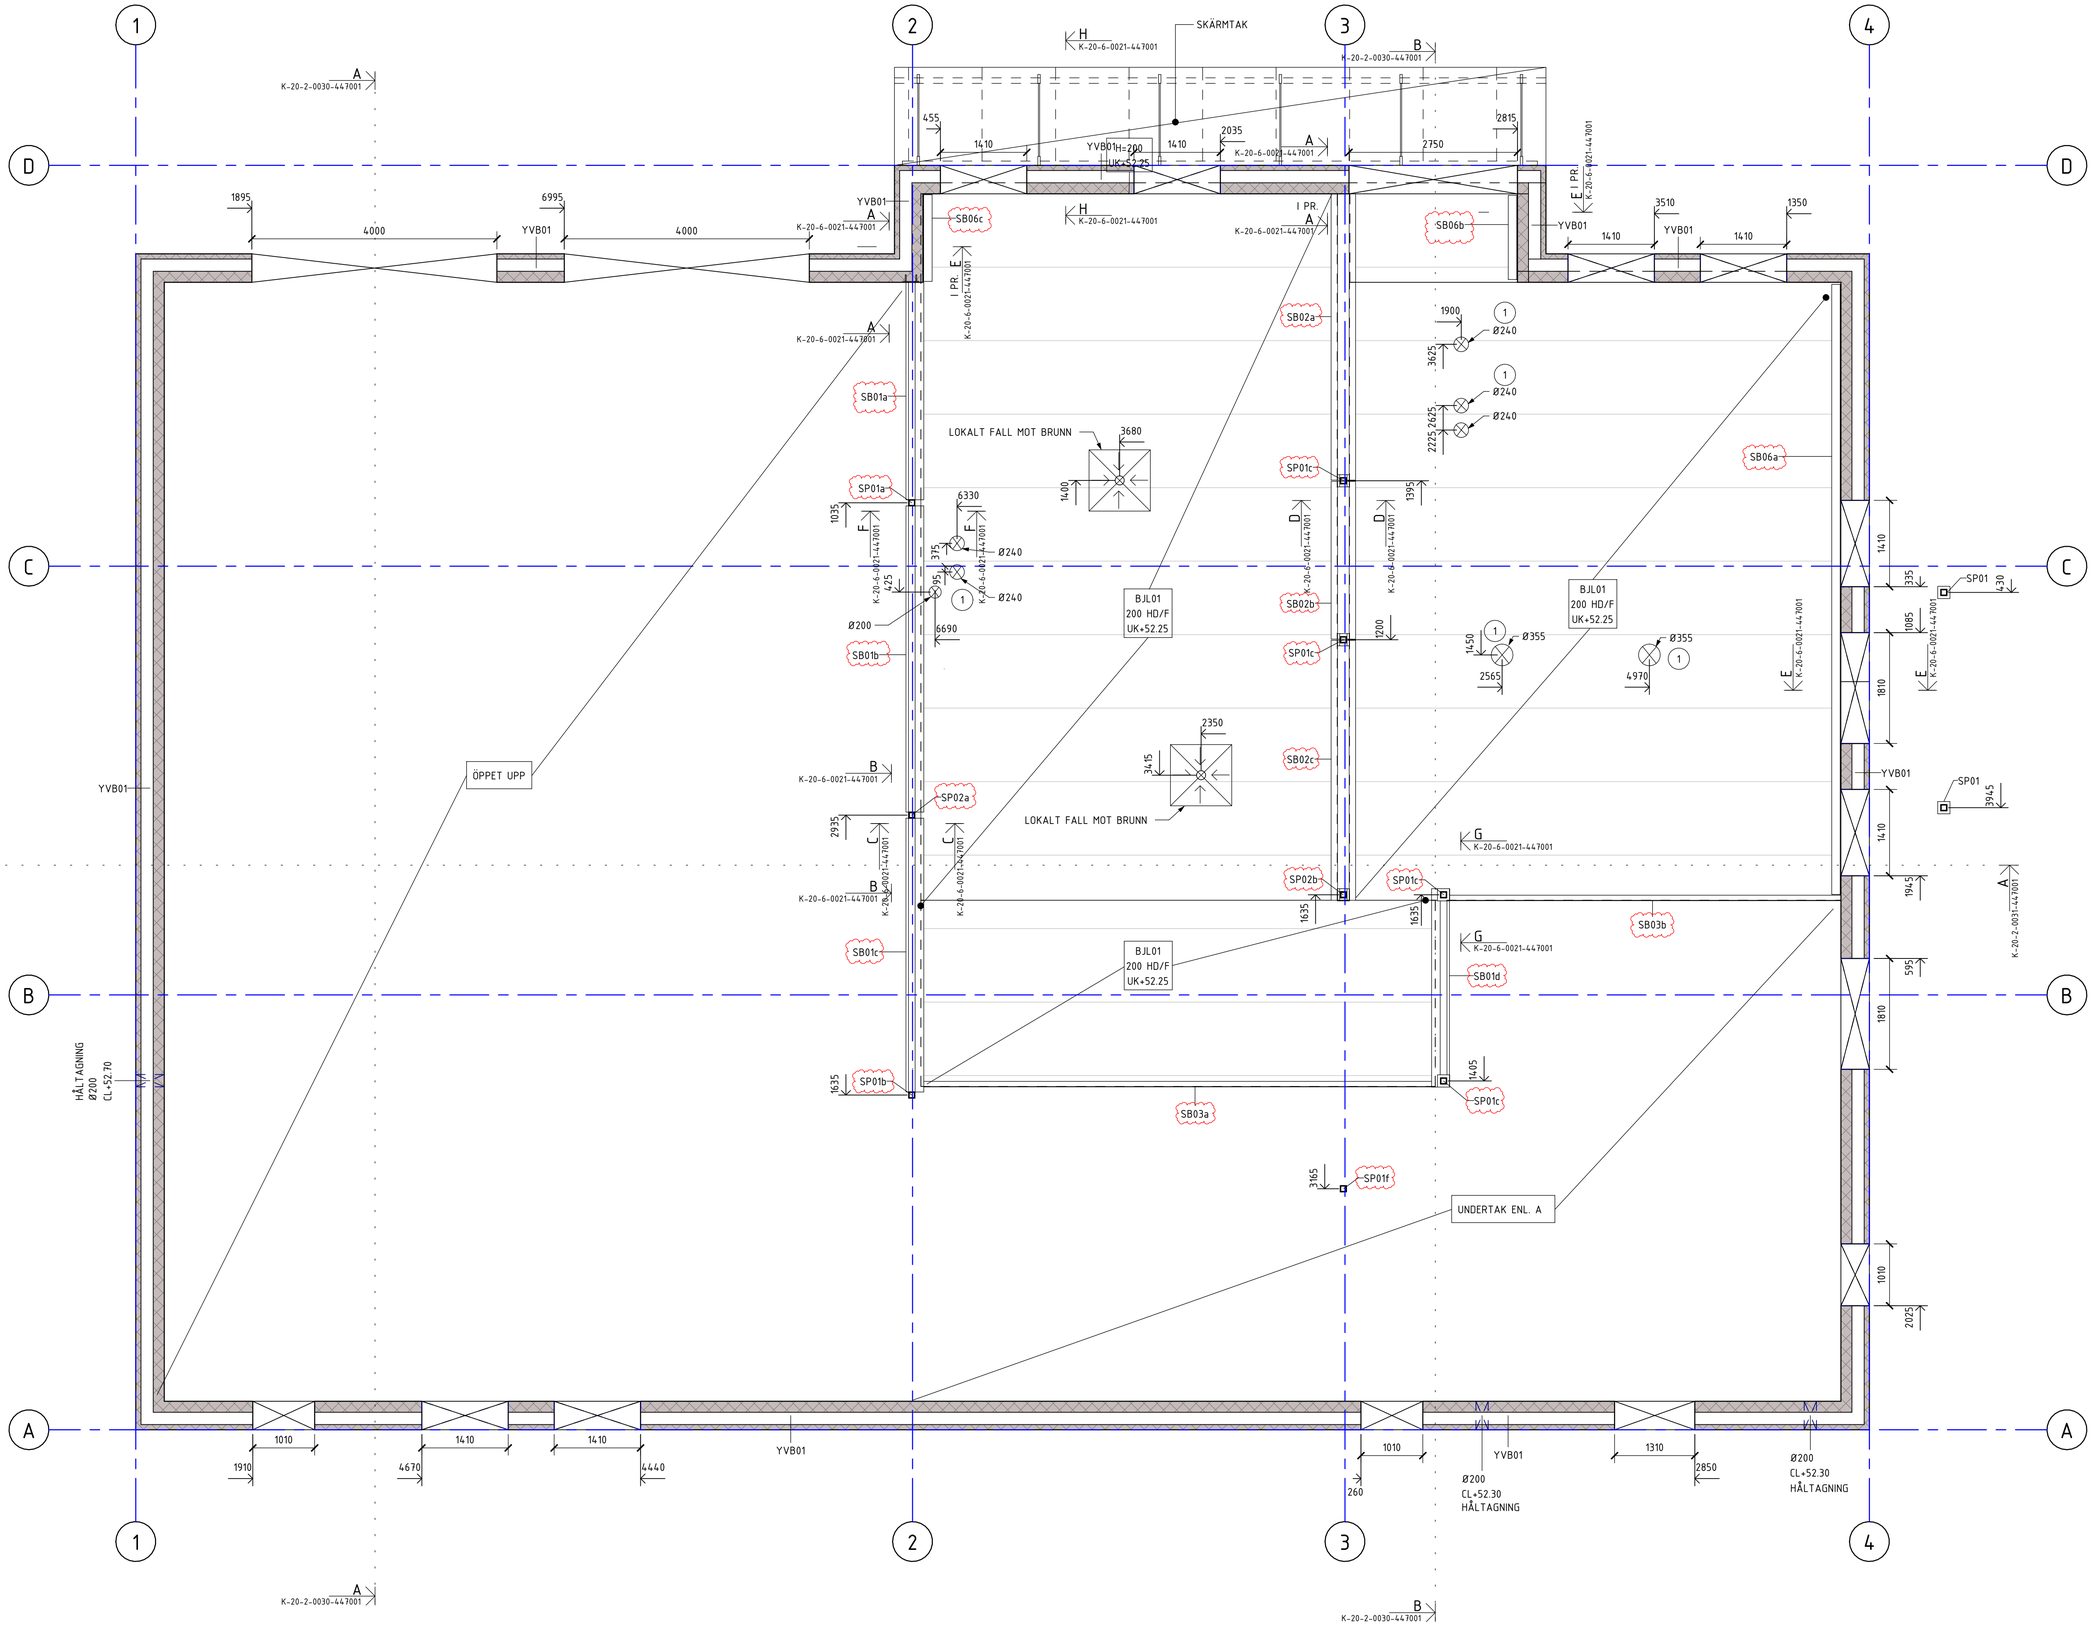

FÖRKLARINGAR

YVB= YTTERVÄGG BÄRANDE
BJL= BJÄLKLAG
YT= YTTERTAK

SP##= STÅLPELARE, SE K-24-6-005X-447001
SB##= STÅLBALK, SE K-24-6-005X-447001

SP01: 100x100x6.3
SP02: 100x100x10
SB01: FSB-170: 110x270 25/15-8
SB02: HSQ-160: 200x400 20/10-5
SB03: UPE 240
SB04: HEA 240
SB05: HEA 220

(1) = EXAKT PLACERING AV HÅL SAMORDNAS MED HÅLDÄCKSLEVERANTÖR

ÖK BETONG VID UPPLAG AV LÄTTELEMENT SKALL SAMORDNAS MED PREFAB.

OBS!! LOKALA FALL UTFÖRS MOT BRUNNAR DIMENSIONER PÅ BRUNNAR ENLIGT VS.

FÖRESKRIFTER

SE RITNING	K-00-0-000x-447001

HÄNVISNINGAR

FÖRESKRIFTER	K-00-0-000x-447001
HUVUDSEKTIONER	K-20-2-0030-447001
HUVUDSEKTIONER	K-20-2-0031-447001
VÄGG- & BJÄLKLAGSTYPER	K-20-6-0020-447001
STOMDETALJER	K-20-6-0021-447001
UPPSTÄLLNING, SB01-SB02	K-24-6-0050-447001
UPPSTÄLLNING, SB03-SB06	K-24-6-0051-447001
UPPSTÄLLNING, SP01	K-24-6-0052-447001
UPPSTÄLLNING, SP02	K-24-6-0053-447001
TAKPLAN	K-41-1-0300-447001
TAKTYPER	K-41-6-0040-447001
TAKDETALJER	K-41-6-0041-447001
TAKDETALJER	K-41-6-0042-447001

A	K-PM02	2026-03-27	LS
BET	ÄNDRINGEN AVSER	DATUM	SIGN

SEKTION

ORIENTERINGSFIGUR

STATUS
GODKÄND

HANDLING
BYGGHANDLING

DATUM	GODKÄND AV	ÄNDRINGS PM
2025-12-12	ANDERS HEDBERG	

BESTÄLLARE
TIERPS KOMMUNFASTIGHETER

PROJEKTNAMN
SÖDERFORS BRANDSTATION

OMRÅDE
TIERP, SÖDERFORS

PROJEKTNUMMER	ADRESS
22447001	TIERPSVÄGEN
DIARIENUMMER	FASTIGHET
	JÖRSÖN 9:4
DISCIPLIN	FÖRETAG
K	KÅVER OCH MELLIN AB
UPPDRAGSNUMMER	SKAPAD AV
24370	MIMI DROTTE
TELEFON	KONTAKTPERSON
073-330 87 06	ANDERS HEDBERG
BYGGNADSVERK	PLUSHUS (NH 2000)
VÅNINGSPLAN / VÅNINGSDEL	DELOMRÅDE

SYSTEM
20-SAMMANSATT REDOVISNING BÄRVERK

SPECIFIKATION
BJÄLKLAG ÖVER PLAN 1

RITNINGSKATEGORI	SKALA	FORMAT
PLAN	1:50	A1

DOKUMENTNUMMER
K-20-1-0100-447001
ÄNDRING
A

2026-03-27 13:26:21

FILNAMN: C:\Users\ludvig.sundqvist\OneDrive - Kåver Mellin AB\Dokument\24370 - Söderfors brandstation_ludvig.sundqvistUEYGS.rvt