


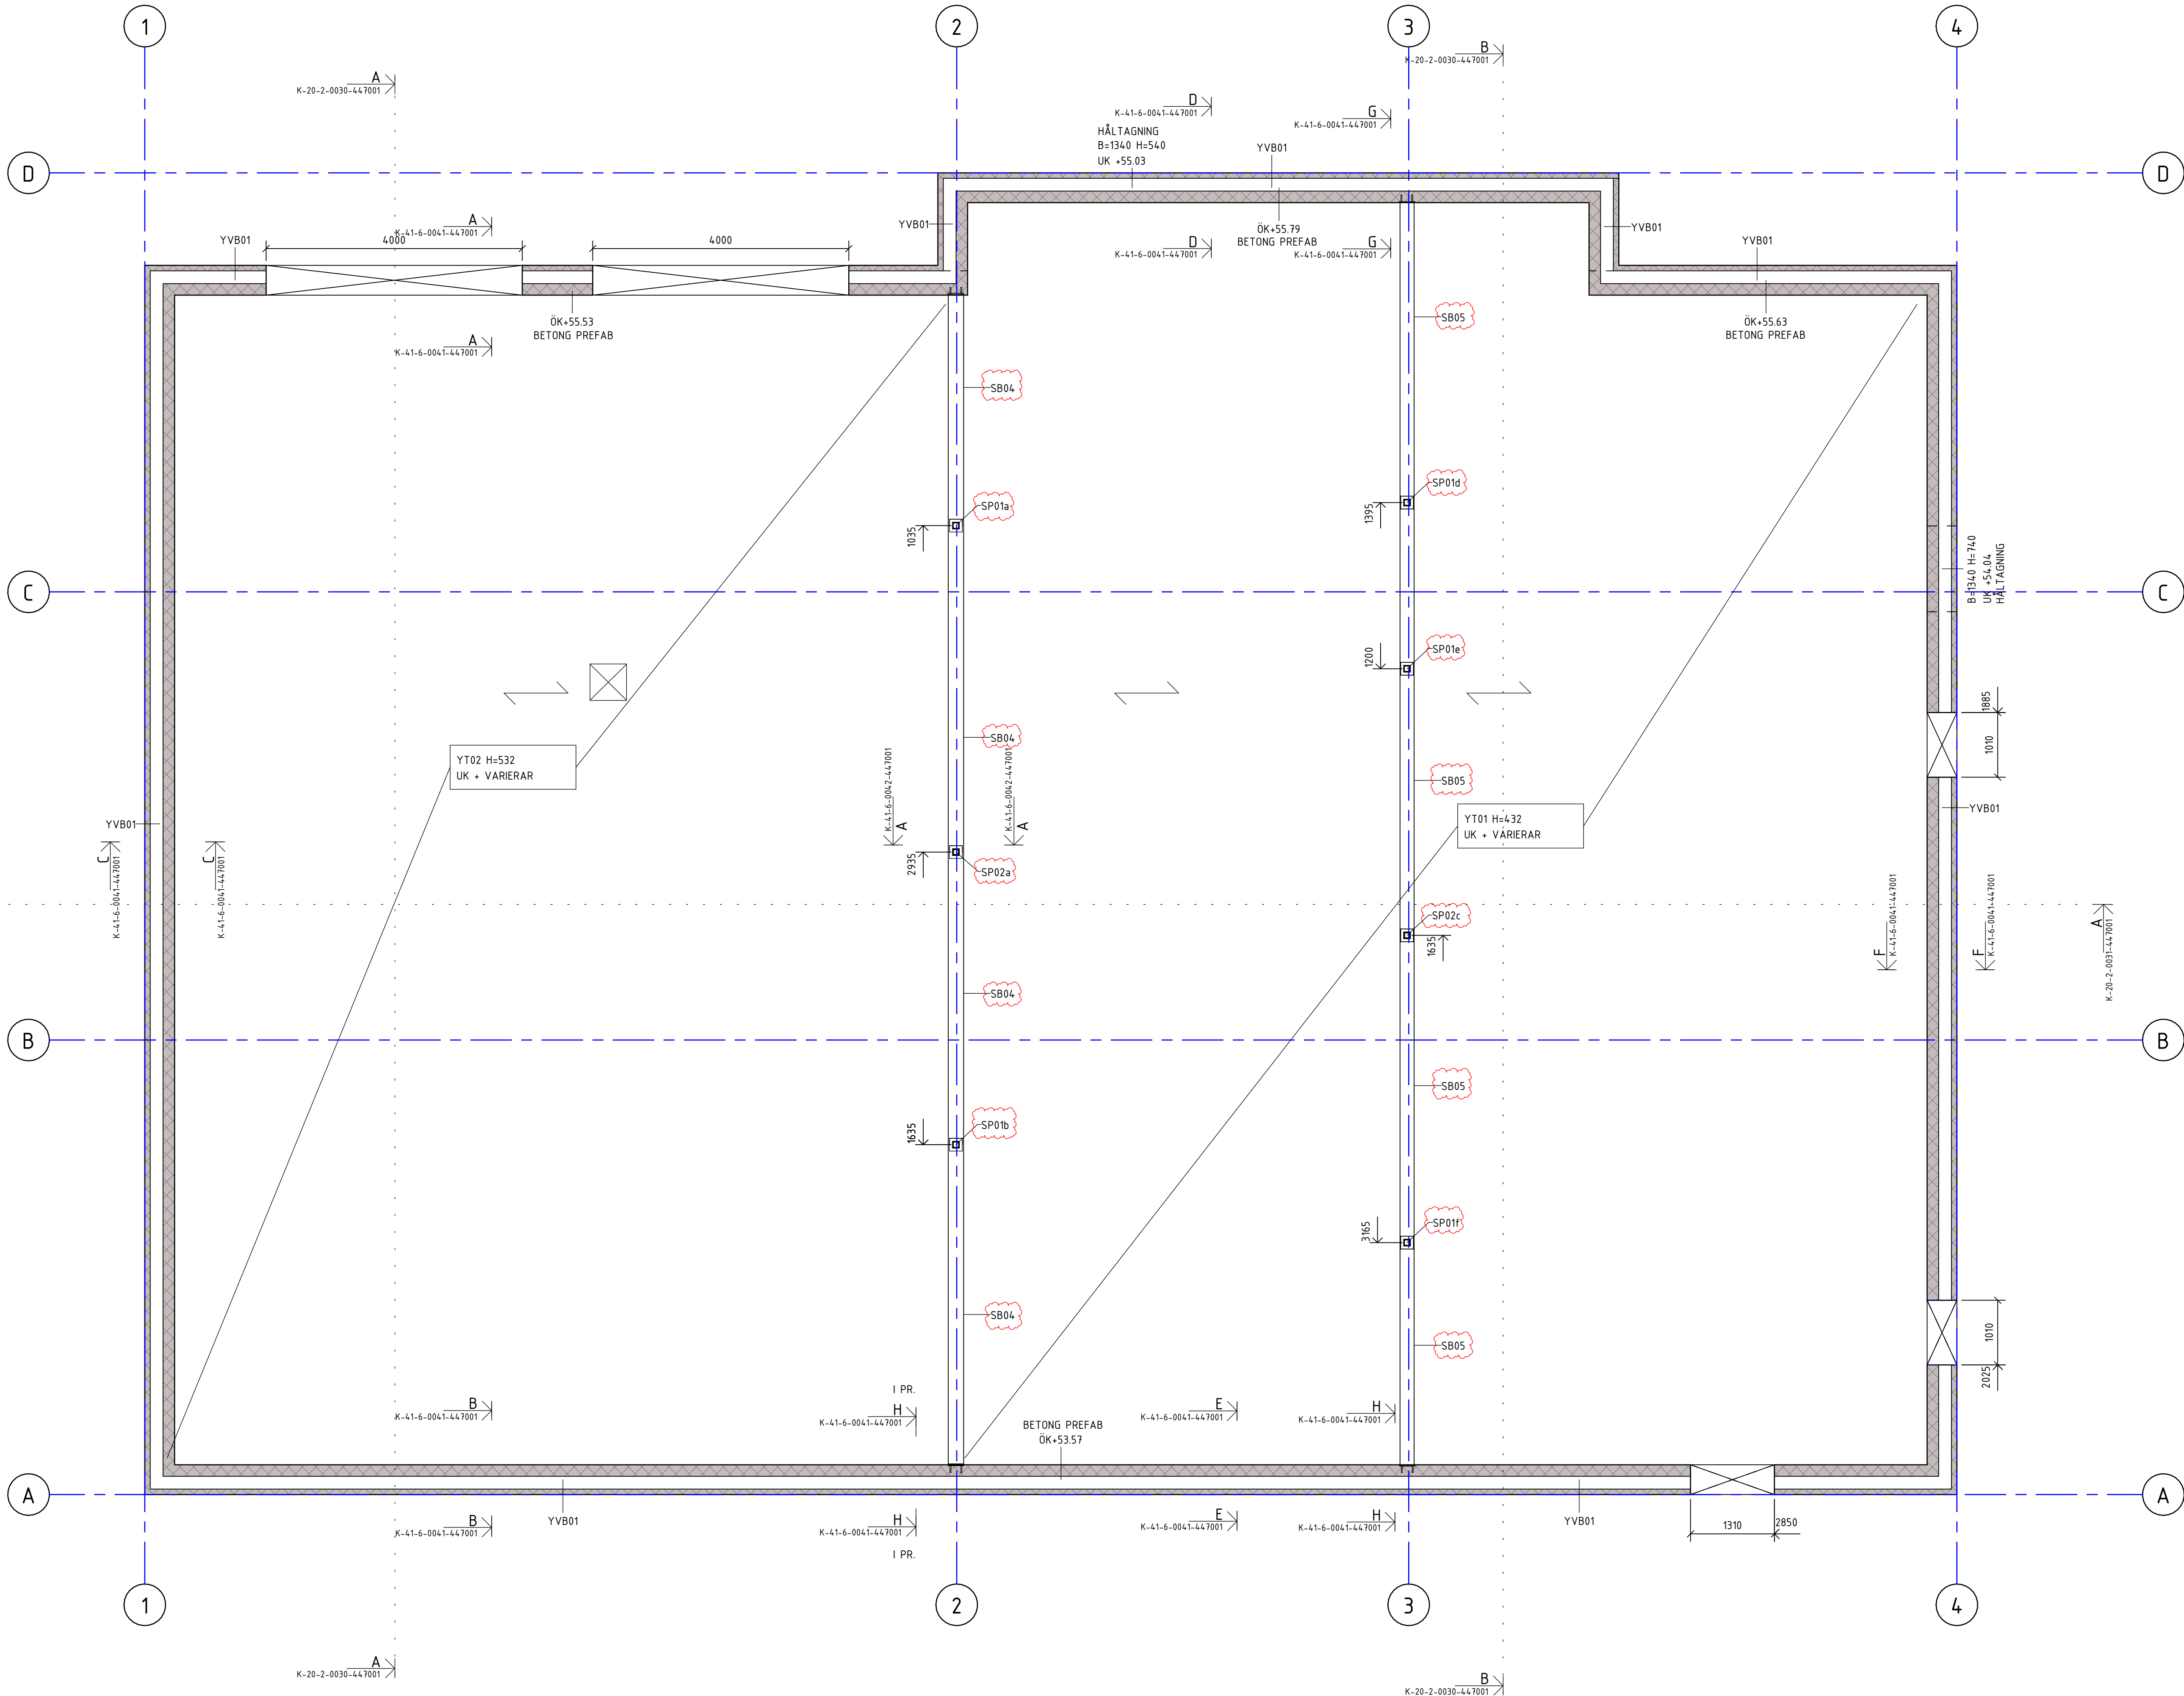

FÖRKLARINGAR

YVB= YTTERVÄGG BÄRANDE
BJL= BJÄLKLAG
YT= YTTERTAK

SP##= STÅLPELARE, SE K-24-6-005X-447001
SB##= STÅLBALK, SE K-24-6-005X-447001

SP01: 100x100x6.3
SP02: 100x100x10
SB01: FSB-170: 110x270 25/15-8
SB02: HSQ-160: 200x400 20/10-5
SB03: UPE 240
SB04: HEA 240
SB05: HEA 220

1 = EXAKT PLACERING AV HÅL
SAMORDNAS MED HÅLÄCKSLIVERANTÖR

ÖK BETONG VID UPPLAG AV LÄTTELEMENT SKALL
SAMORDNAS MED PREFAB.

OBS!! LOKALA FALL UTFÖRS MOT BRUNNAR
DIMENSIONER PÅ BRUNNAR ENLIGT VS.

FÖRESKRIFTER


SE RITNING K-00-0-000x-447001

HÄNVISNINGAR


FÖRESKRIFTER K-00-0-000x-447001
HUVUDSEKTIONER K-20-2-0030-447001
HUVUDSEKTIONER K-20-2-0031-447001
VÄGG- & BJÄLKLAGSTYPER K-20-6-0020-447001
STOMDETALJER K-20-6-0021-447001
UPPSTÄLLNING, SB01-SB02 K-24-6-0050-447001
UPPSTÄLLNING, SB03-SB06 K-24-6-0051-447001
UPPSTÄLLNING, SP01 K-24-6-0052-447001
UPPSTÄLLNING, SP02 K-24-6-0053-447001
TAKPLAN K-41-1-0300-447001
TAKTYPER K-41-6-0040-447001
TAKDETALJER K-41-6-0041-447001
TAKDETALJER K-41-6-0042-447001

A	K-PM02	2026-03-27	LS
BET	ÄNDRINGEN AVSER	DATUM	SIGN

SEKTION

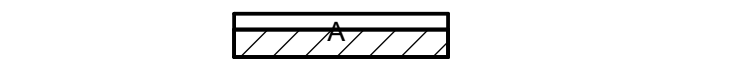

ORIENTERINGSFIGUR

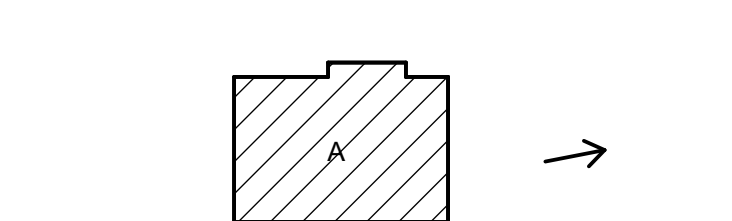

STATUS

GODKÄND

HANDLING

BYGGHANDLING

DATUM 2025-12-12

SKAPAD AV ANDERS HEDBERG

ÄNDRINGS PM

BESTÄLLARE

TIERPS KOMMUNFASTIGHETER

PROJEKTNAMN

SÖDERFORS BRANDSTATION

VARIAZE

TIERP, SÖDERFORS

PROJEKTNUMMER 22447001

ADRESS TIERPSVÄGEN

SHARENUMMER

FASTIGHET JÖRSÖN 9:4

DISCIPLIN K

FÖRETAG KÄVER OCH MELLIN AB

UPPDRAGSRUMMER 24370

SKAPAD AV MIMI DROTTE

TELEFON 073-330 87 06

KONTAKTPERSON ANDERS HEDBERG

BYGGNADSRISIK

PLÅNSHED (PM 2006)

VÄNINGSPLAN

VÄNINGSDEL

DELOMRÅDE

SYSTEM

20-SAMMANSATT REDOVISNING BÄRVERK

PREGERATION

BJÄLKLAG ÖVER PLAN 2

TYTTERSEKTION

PLAN

SKALA 1:50

FORMAT A1

ANDRING

OKUMENTNUMMER

K-20-1-0200-447001

A

