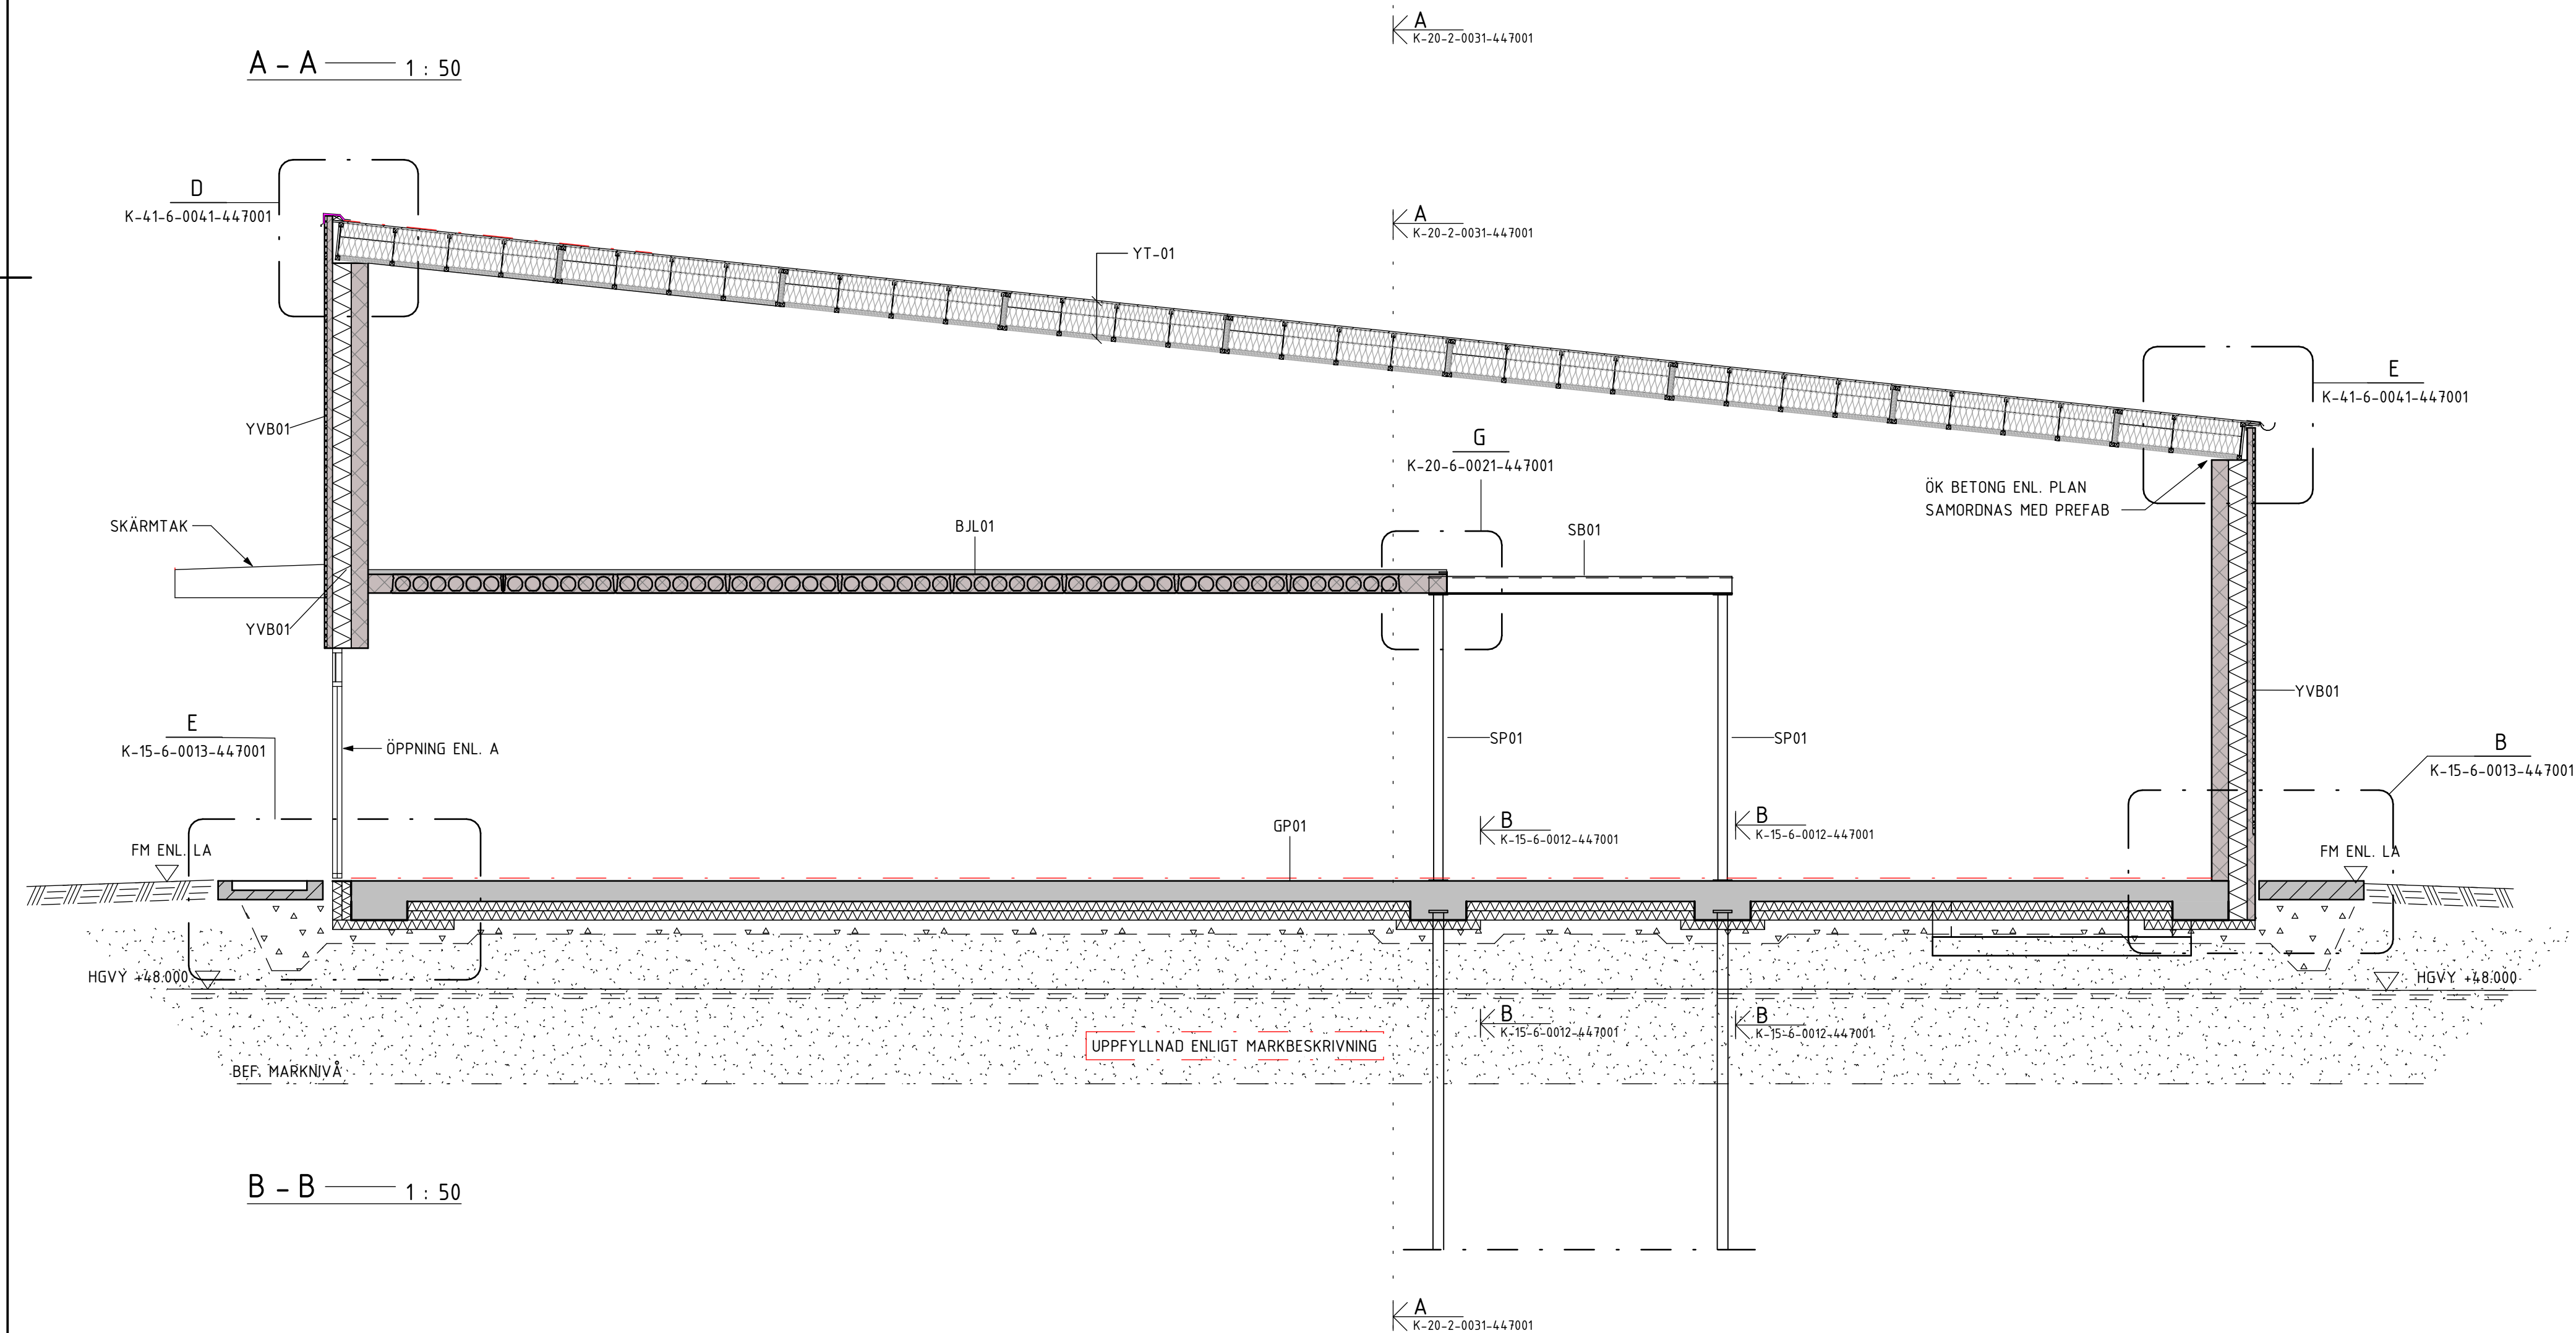


FÖRKLARINGAR

GP= GRUNDPLATTA
YVB= YTTERVÄGG BÄRANDE
BJL= BJÄLKLAG
YT= YTTERTAK

SP= STÅLPELARE
SB= STÅLBALK


HGVY = HÖGSTA UPPMÄTTA GRUNDVATTENYTAN

FÖRESKRIFTER

SE RITNING K-00-0-000x-447001

HÄNVISNINGAR

FÖRESKRIFTER	K-00-0-000x-447001
TYPEDETALJER GRUND	K-15-6-0010-447001
TYPEDETALJER PÅLFUNDAMENT	K-15-6-0011-447001
GRUNDETALJER	K-15-6-0012-447001
GRUNDETALJER	K-15-6-0013-447001
VÄGG- & BJÄLLAGSTYPER	K-20-6-0020-447001
STOMDETALJER	K-20-6-0021-447001
TAKTYPER	K-41-6-0040-447001
TAKDETALJER	K-41-6-0041-447001

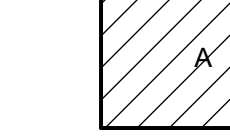SEKTION		
		
ORIENTERINGSSKISS		
		
STATUS		
HANDLING		
GODKÄND		
BYGGHANDLING		
DATUM	ÖSKAND AV	ÄNDRINGS PM
2025-12-12	ANDERS HEDBERG	
BESTÄLLARE		
		
PROJEKTNAMN		
SÖDERFORS BRANDSTATION		
OMRÅDE		
TIERP, SÖDERFORS		
PROJEKTNUMMER	ADRESS	
22447001	TIERPSVÄGEN	
DÄRRENUMMER	FASTIGHET	
	JÖRSÖN 9:4	
DISCIPLIN	FÖRETAG	
K	KÄVER OCH MELLIN AB	
LIVSRÅDNUMMER	STRÅD AV	
24370	MIMI DROTTE	
TELEFON	KONTAKTPERSON	
073-330 87 06	ANDERS HEDBERG	
BYGGNADSVÄRK	FLUSHJUD (RH 2000)	
VÄNINGSPLAN	VÄNINGSDETEL	DELÖMRÅDE
SYSTEM		
20-SAMMANSATT REDOVISNING BÄRVERK		
SPECIFIKATION		
HUVUDSEKTIONER		
ÄTTHUSKATEGORI	SKALA	FORMAT
SEKTION	1:50	A1
DOKUMENTNUMMER	ÄNDRING	
K-20-2-0030-447001		