


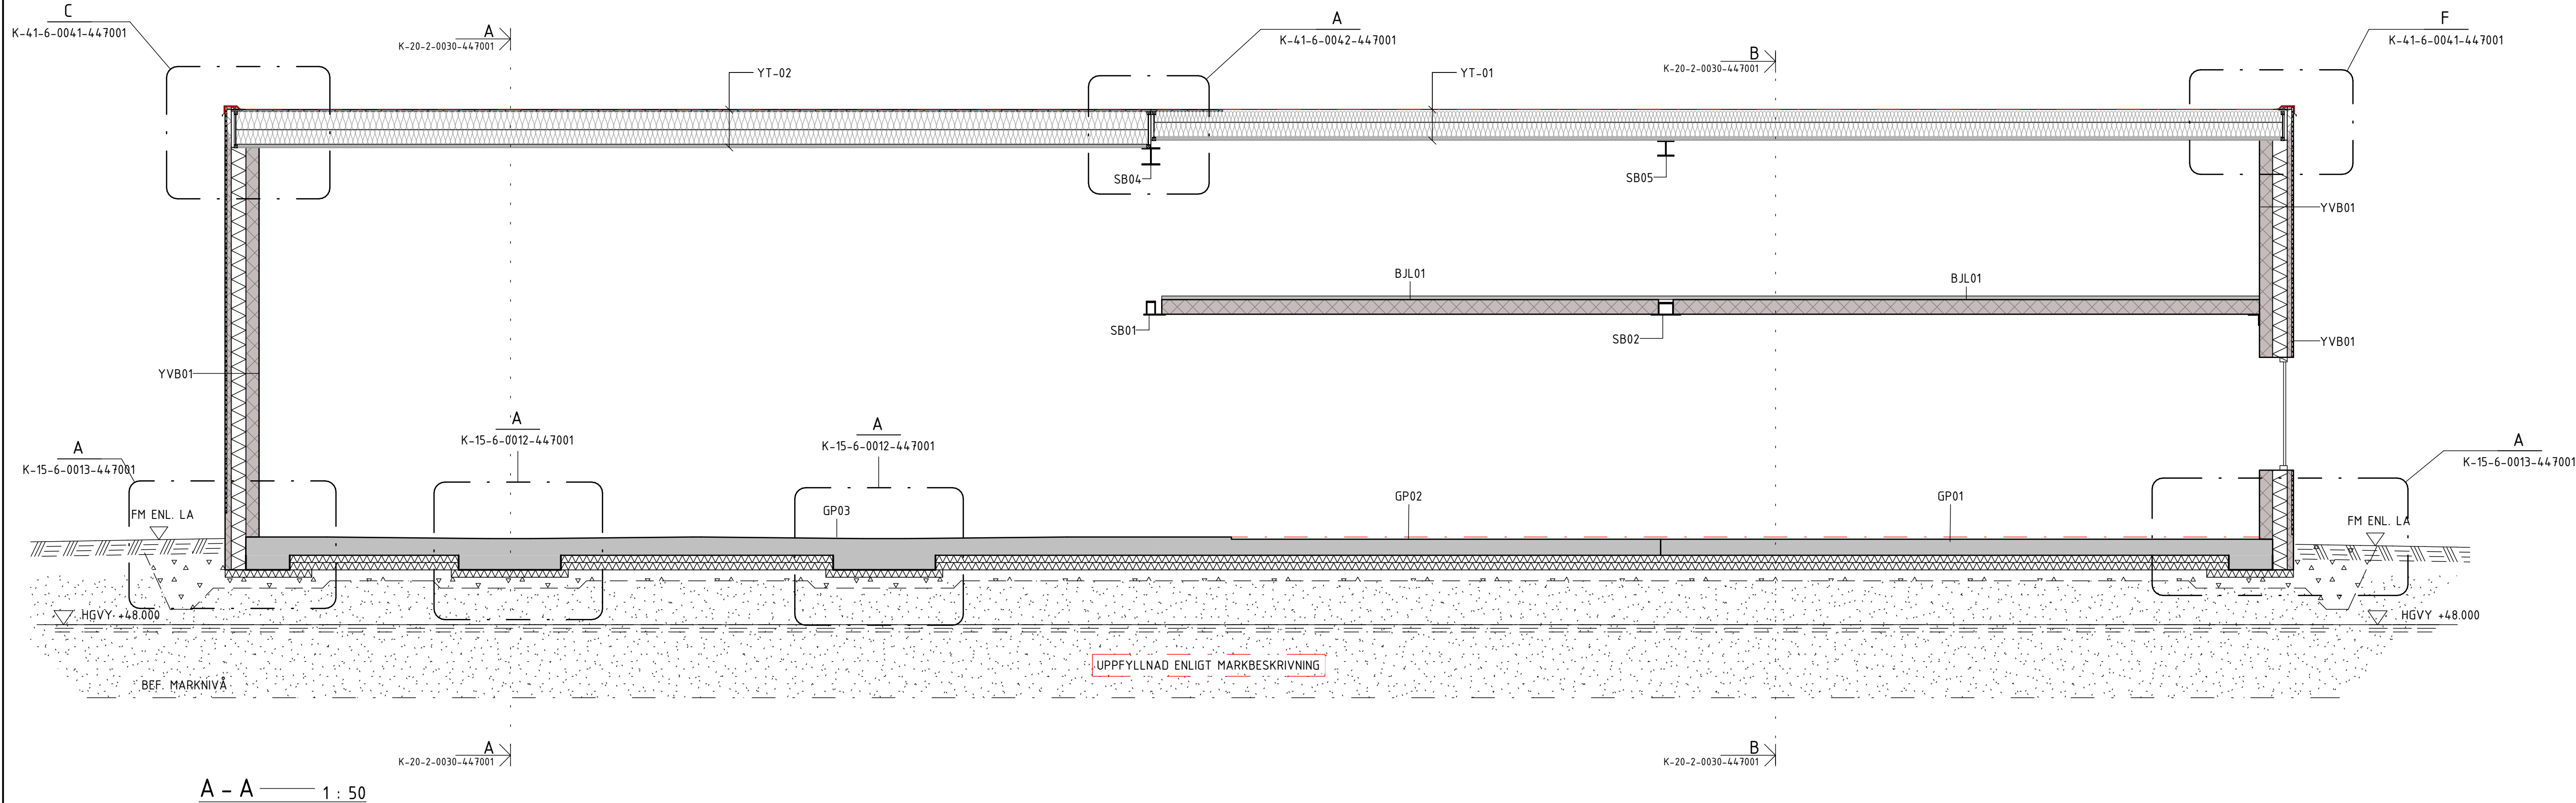

FÖRKLARINGAR

GP= GRUNDPLATTA
YVB= YTTERVÄGG BÄRANDE
BJL= BJÄLKLAG
YT= YTERTAK

SP= STÅLPELARE
SB= STÅLBALK

HGVY = HÖGSTA UPPMÄTTA GRUNDVATTENYTAN

FÖRESKRIFTER

SE RITNING K-00-0-000x-447001

HÄNVISNINGAR

FÖRESKRIFTER K-00-0-000x-447001
TYPDETALJER GRUND K-15-6-0010-447001
TYPDETALJER PÄLFUNDAMENT K-15-6-0011-447001
GRUNDETALJER K-15-6-0012-447001
GRUNDETALJER K-15-6-0013-447001
VÄGG- & BJÄLKLAGSTYPER K-20-6-0020-447001
STOMDETALJER K-20-6-0021-447001
TAKTYPER K-41-6-0040-447001
TAKDETALJER K-41-6-0041-447001

SEKTION		
ORIENTERINGSFIGUR		
STATUS		
GODKÄND		
HANDLING		
BYGGHANDLING		
DATUM	SKAPAD AV	ÄNDRINGS FM
2025-12-12	ANDERS HEDBERG	
BESTÄLLARE		
PROJEKTNAMN		
SÖDERFORS BRANDSTATION		
OMRÅDE		
TIERP, SÖDERFORS		
PROJEKTNUMMER	ADRESS	
22447001	TIERPSVÄGEN	
DIARIENUMMER	FASTIGHET	
	JÖRSÖN 9:4	
DISCIPLIN	FÖRETAG	
K	KÄVER OCH MELLIN AB	
UPPRORSGRUMMER	SKAPAD AV	
24370	MIMI DROTTE	
TELEFON	KONTAKTPERSON	
073-330 87 06	ANDERS HEDBERG	
BYGGNADSTYP	PLÅNEN (BY 2005)	
VÄNINGSPLAN	VÄNINGSDEL	DELOMRÅDE
SYSTEM		
20-SAMMANSATT REDOVISNING BÄRVERK		
SPECIFIKATION		
HUVUDSEKTIONER		
SEKTION		SKALA
		1:50
FORMAT		ÄNDRING
A1		
DOCUMENTNUMMER		
K-20-2-0031-447001		

