




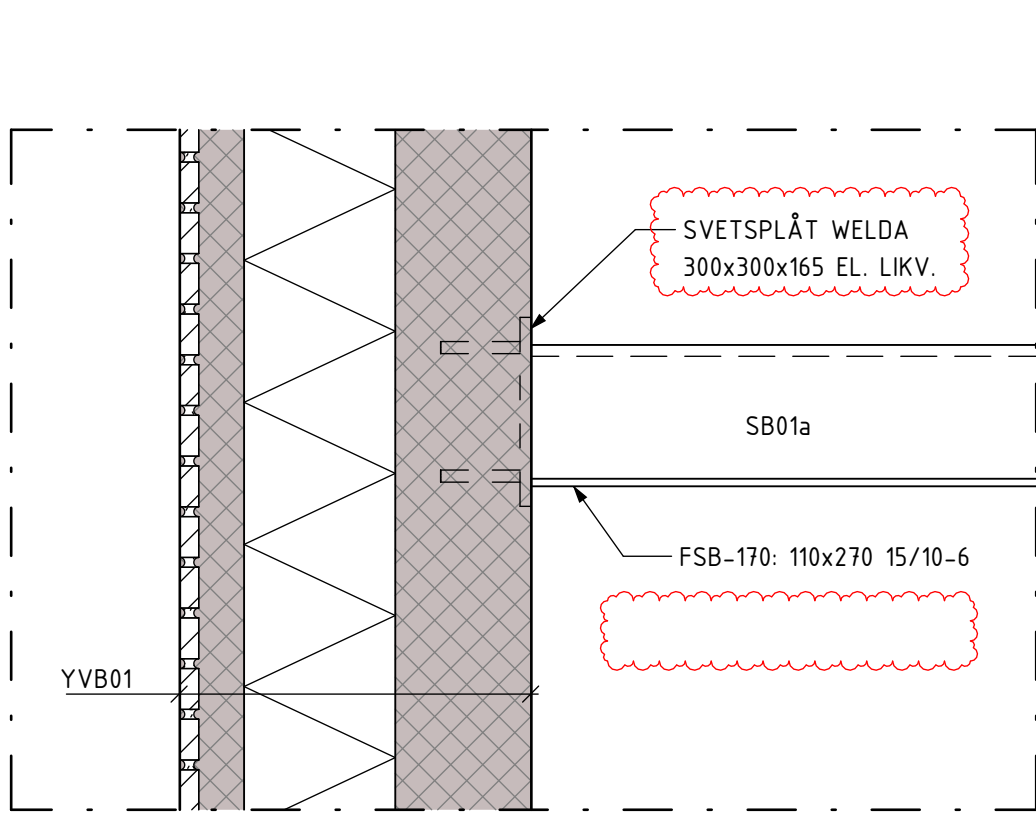


A - A 1 : 10

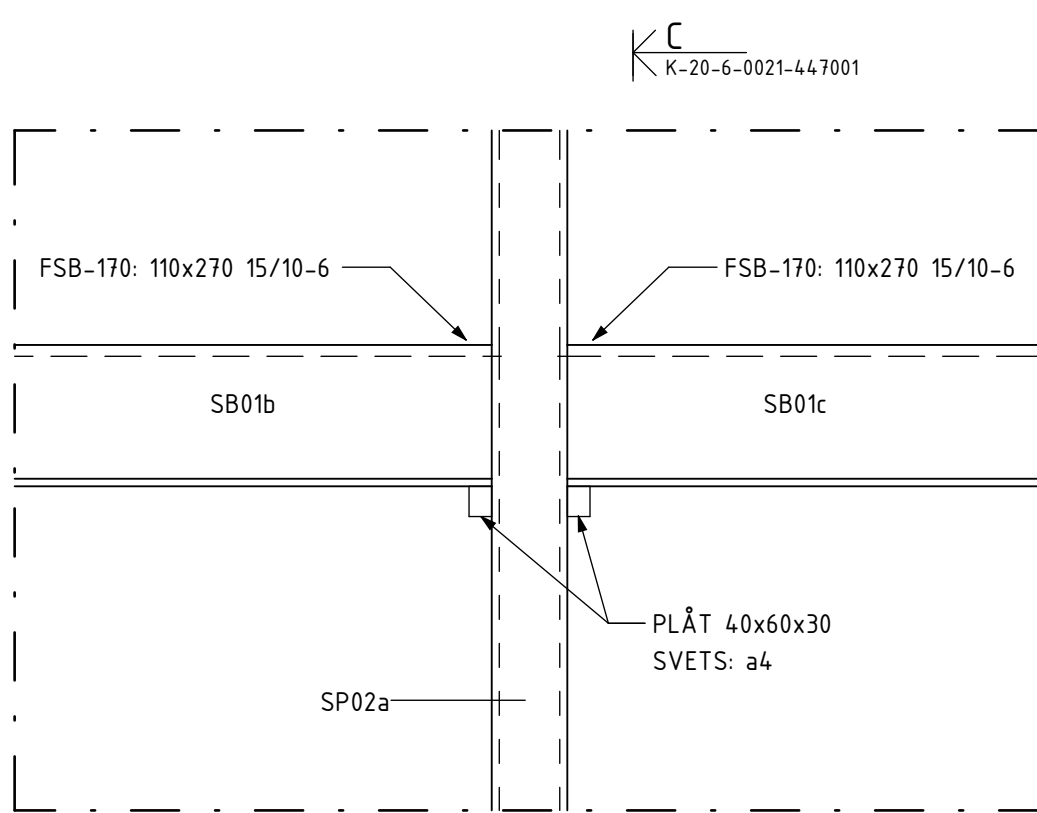


B - B 1 : 10

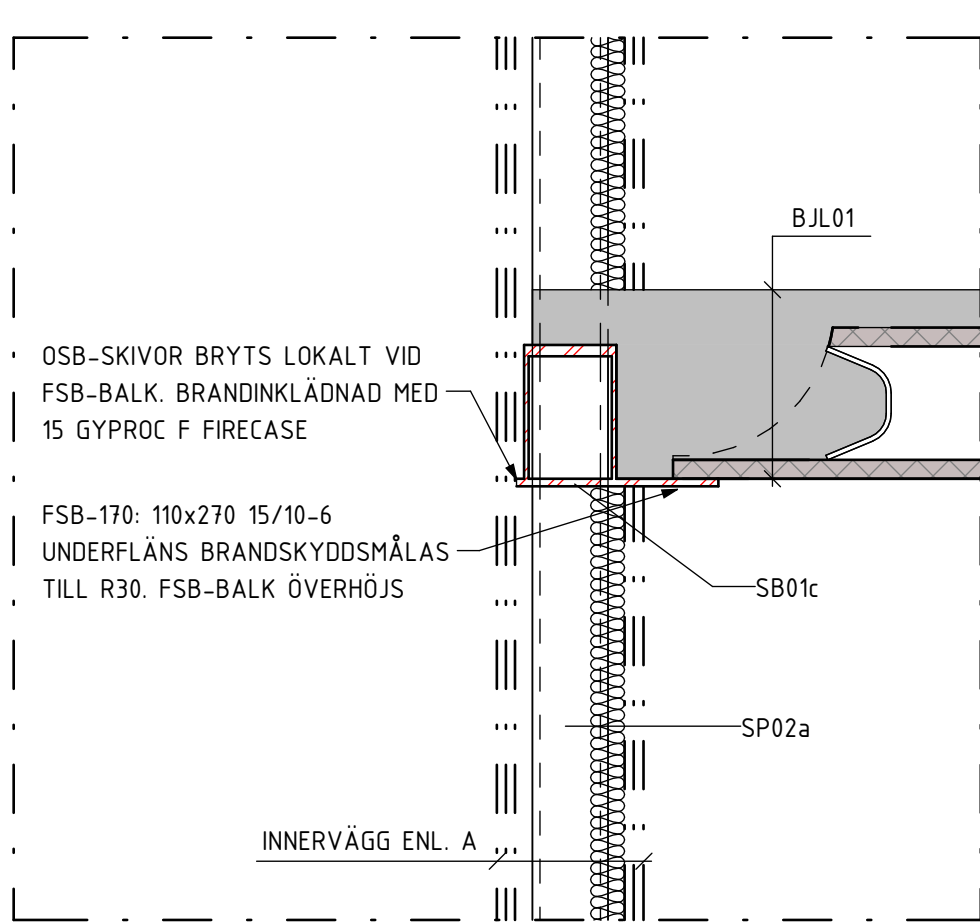


C - C 1 : 10

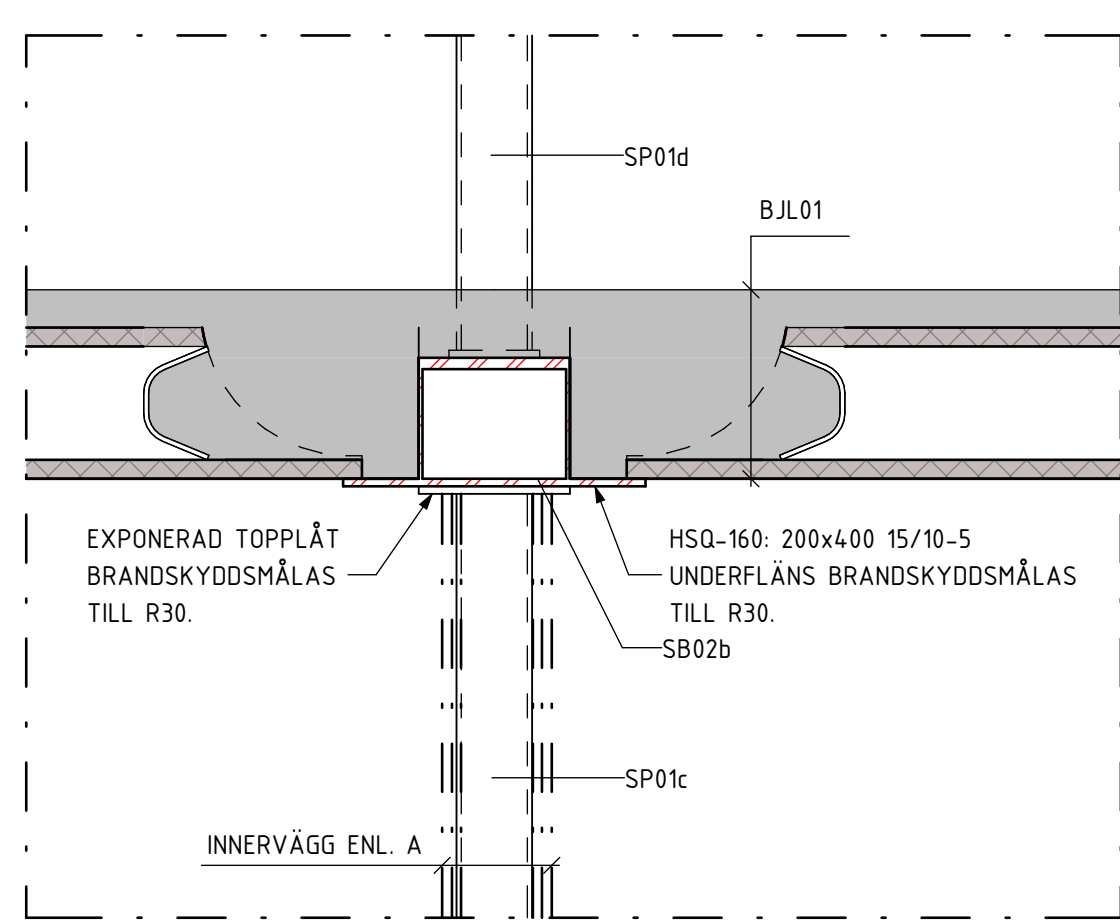


D - D 1 : 10

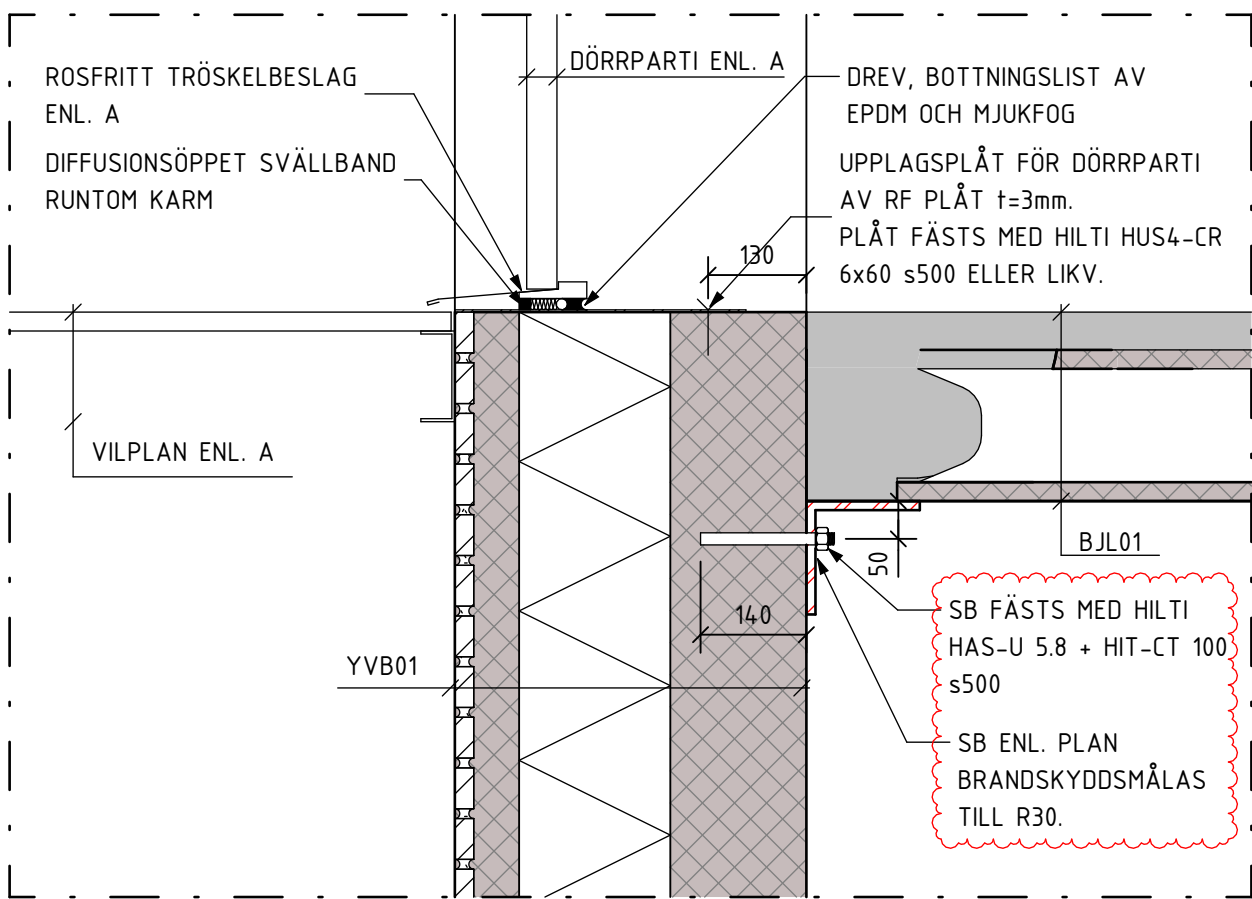


E - E 1 : 10

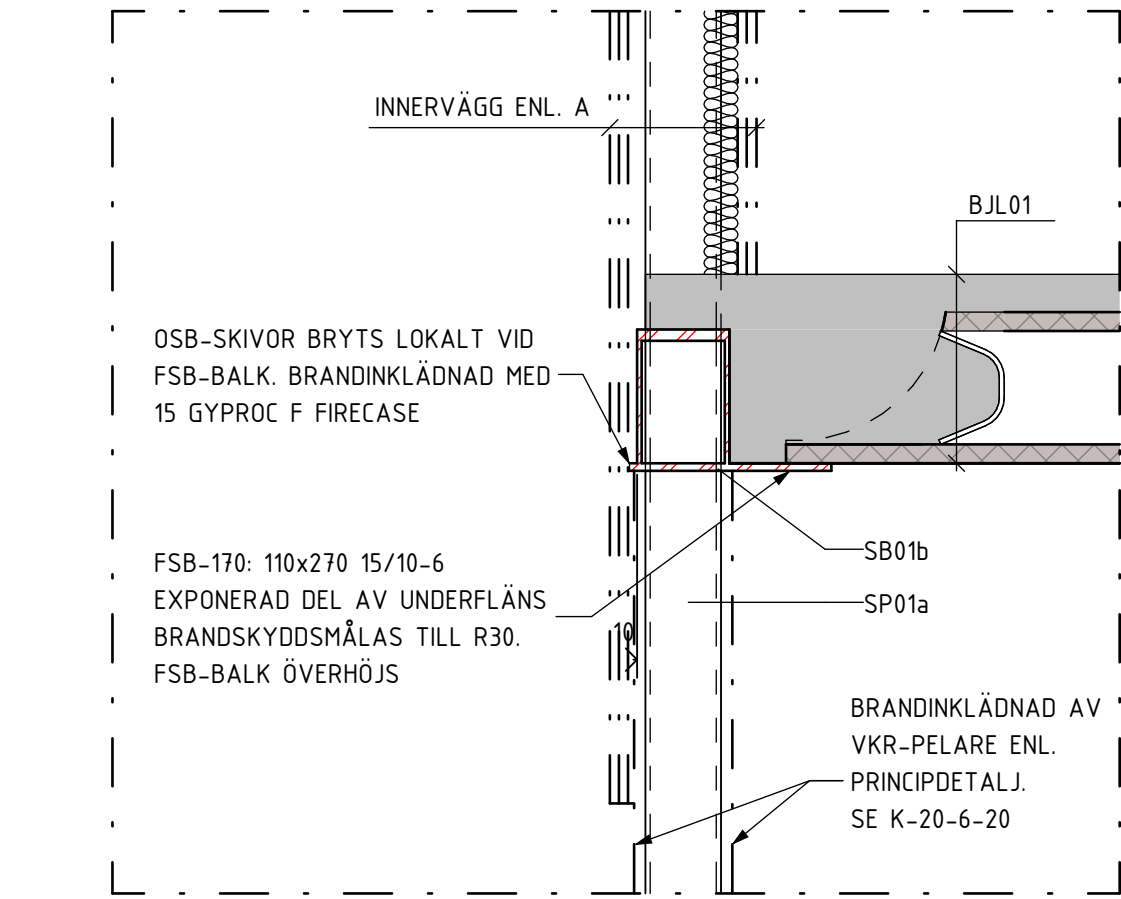

F - F 1 : 10

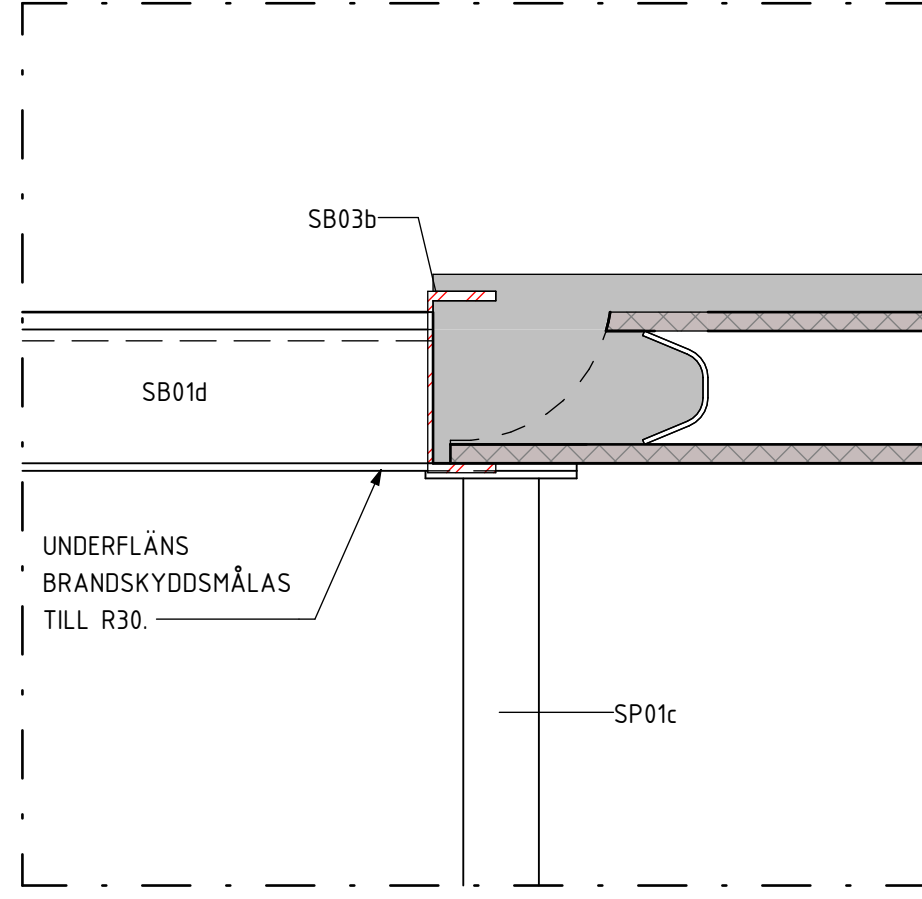


G - G 1 : 10

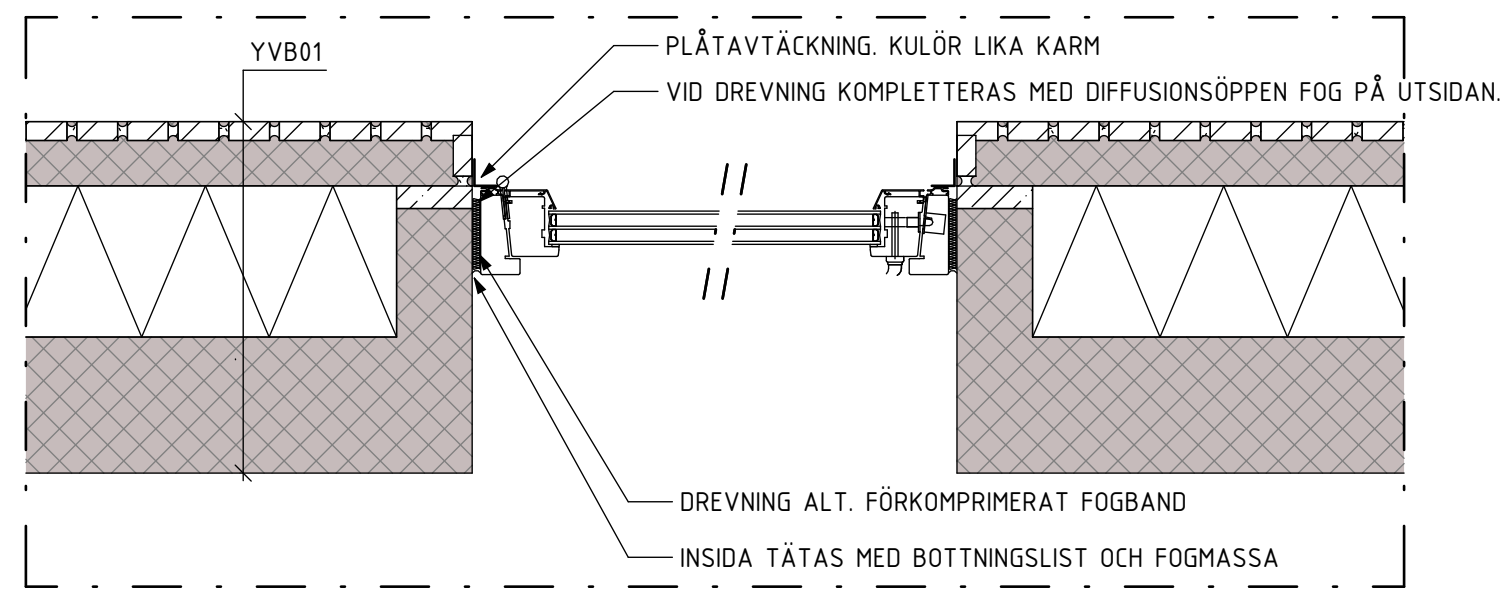


PRINCIP FÖNSTERINFÄSTNING

SKALA 1 : 10

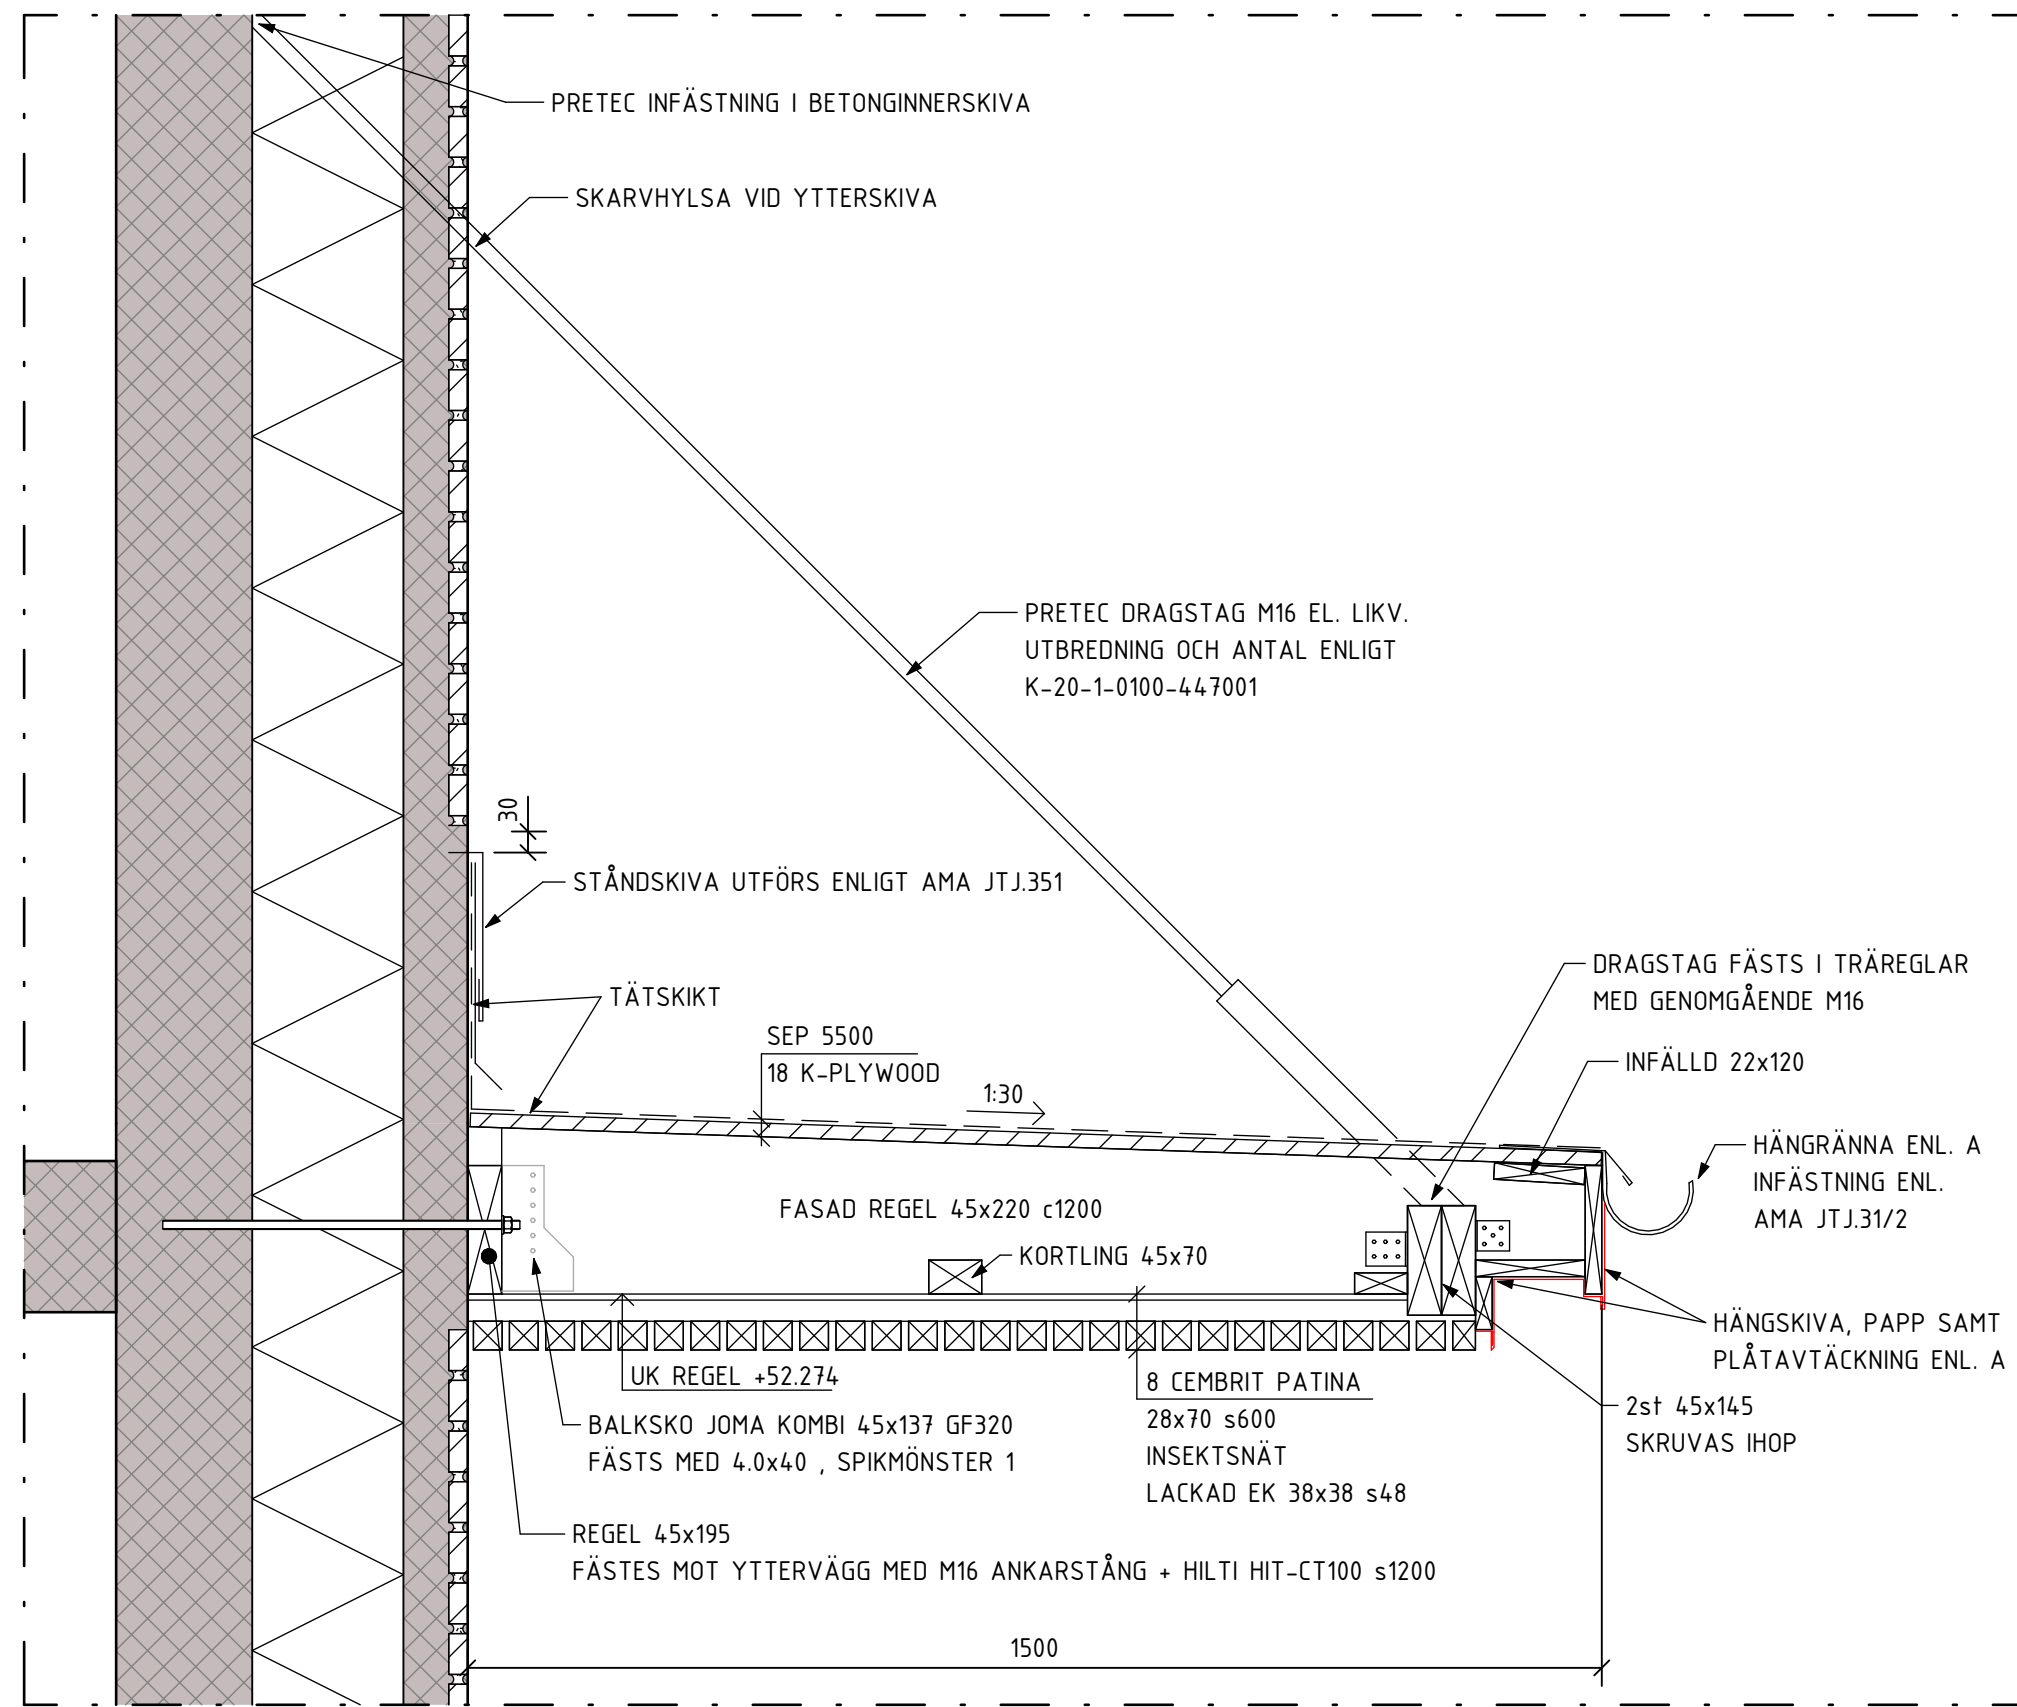

H - H 1 : 10

SKALA 1:10

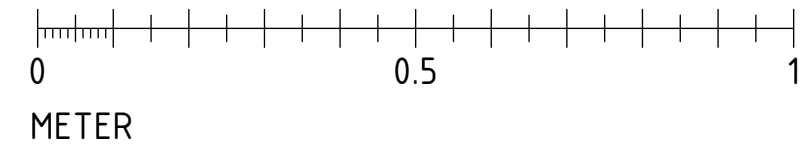

FÖRKLARINGAR

GP= GRUNDPLATTA
YVB= YTTERVÄGG BÄRANDE
BJL= BJÄLKLAG
YT= YTTERTAK

SP##= STÅLPELARE, SE K-24-6-005X-447001
SB##= STÅLBALK, SE K-24-6-005X-447001

FÖRESKRIFTER

SE RITNING


K-00-0-000x-447001

HÄNVISNINGAR

FÖRESKRIFTER
BJÄLKLAG ÖVER PLAN 1 K-20-1-0100-447001
BJÄLKLAG ÖVER PLAN 2 K-20-1-0200-447001
HUVUDSEKTIONER K-20-2-0030-447001
HUVUDSEKTIONER K-20-2-0031-447001
VÄGG- & BJÄLKLAGSTYPER K-20-6-0020-447001
UPPSTÄLLNING, SB01-SB02 K-24-6-0050-447001
UPPSTÄLLNING, SB03-SB06 K-24-6-0051-447001
UPPSTÄLLNING, SP01 K-24-6-0052-447001
UPPSTÄLLNING, SP02 K-24-6-0053-447001

A	K-PM02	2026-03-27	LS
BET	ÄNDRINGEN AVSER	DATUM	SIGN

SEKTION

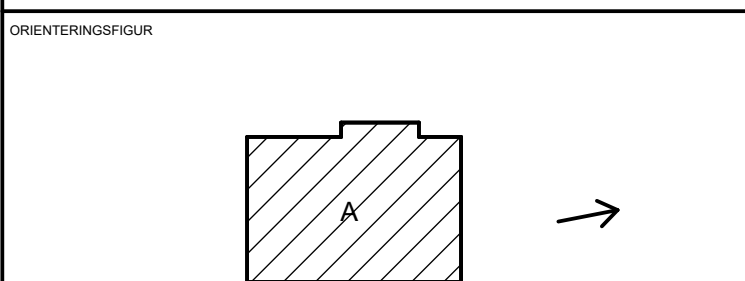

STATUS	GODKÄND
HANDLING	BYGGHANDLING
DATUM	2025-12-12
ANSÖKAN AV	ANDERS HEDBERG
ÄNDRINGS FM	



PROJEKTNAMN	SÖDERFORS BRANDSTATION
OMRÅDE	TIERP, SÖDERFORS

PROJEKTNUMMER	22447001	ADRESS	TIERPSVÄGEN
DIARIENUMMER		FASTIGHET	JÖRSÖN 9:4
DISCIPLIN	K	FÖRETAG	KÄVER OCH MELLIN AB
UPPDRAGSRUMMER	24370	SKAPAD AV	AMANDA WIIK
TELEFON	073-330 87 06	KONTAKTPERSON	ANDERS HEDBERG
BYGGNADSRUMMER		PLÅTAVTÄCKNING	(BYG 2000)

VÄNINGSPLAN	VÄNINGSDEL	DELOMRÅDE
-------------	------------	-----------

SYSTEM		
20-SAMMANSATT REDOVISNING BÄRVERK		
SPECIFIKATION		
STOMDETALJER		
RITNINGSKATEGORI	SKALA	FORMAT
DETALJ	1:10	A1
DOKUMENTNUMMER		ÄNDRING
K-20-6-0021-447001		A