




SB01a — 1:20
FSB-170: 110x270 25/15-8
ANTAL: 1st

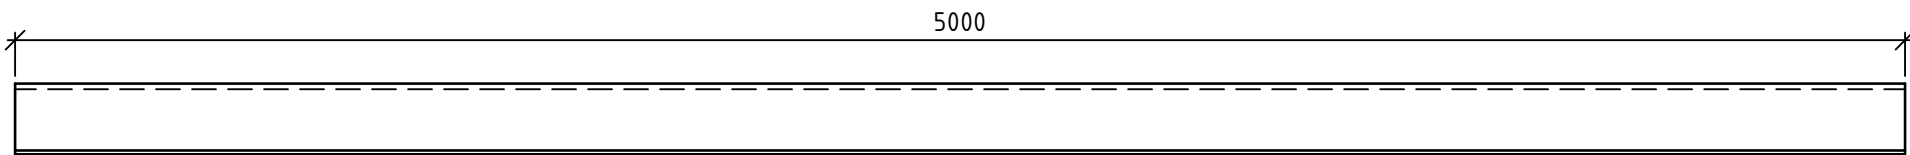


SB01b — 1:20
FSB-170: 110x270 25/15-8
ANTAL: 1st

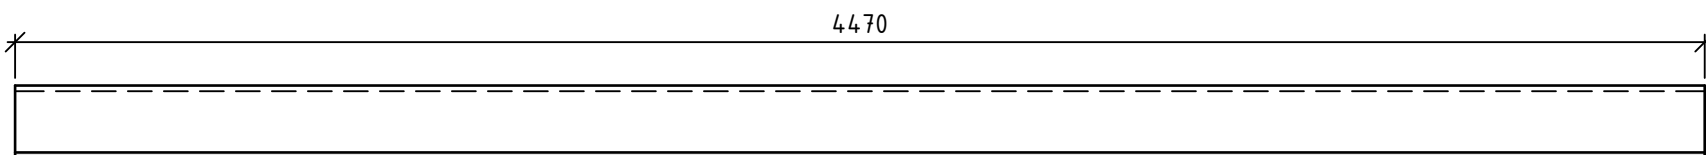


SB01c — 1:20
FSB-170: 110x270 25/15-8
ANTAL: 1st

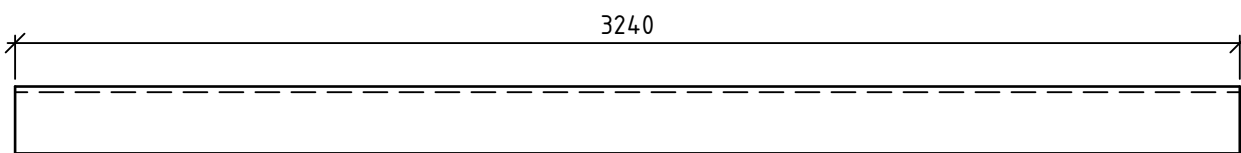


SB01d — 1:20
FSB-170: 110x270 25/15-8
ANTAL: 1st

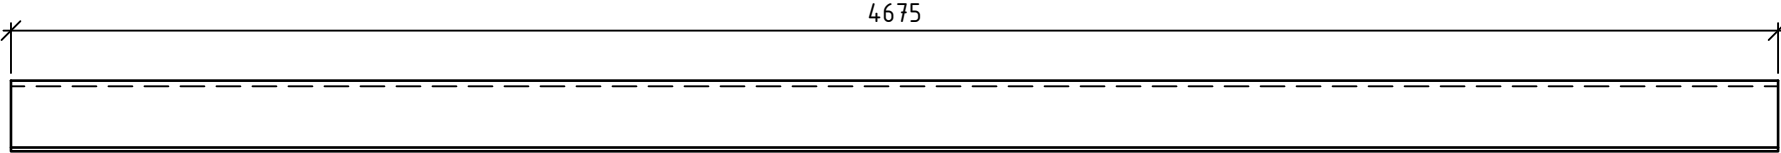


SB02a — 1:20
HSQ-160: 200x400 20/10-5
ANTAL: 1st

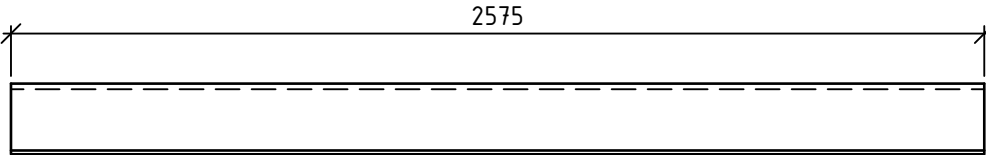

SB02b — 1:20
HSQ-160: 200x400 20/10-5
ANTAL: 1st

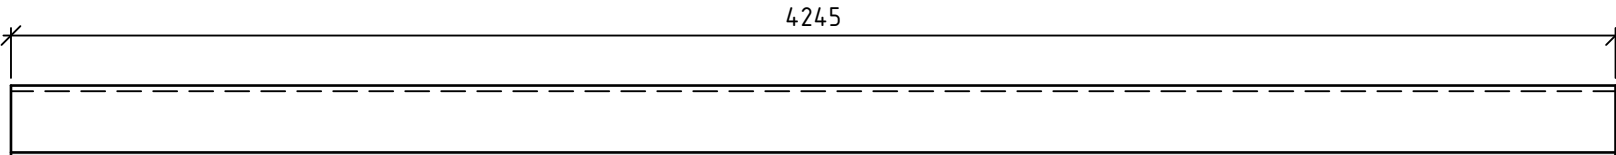

SB02c — 1:20
HSQ-160: 200x400 20/10-5
ANTAL: 1st

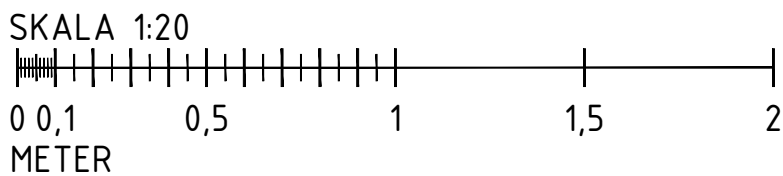

FÖRKLARINGAR

FÖRESKRIFTER

HÄNVISNINGAR

SEKTION		
ORIENTERINGSPIGUR		
STATUS		
GODKÄND		
HANDLING		
BYGGHANDLING		
ANTAG	LODNING AV	ÄNDRINGS PM
2026-03-27	ANDERS HEDBERG	
BESTÄLLARE		
PROJEKTNAMN		
SÖDERFORS BRANDSTATION		
OBJEKT		
TIERP, SÖDERFORS		
PROJEKTNUMMER	ADRESS	
22447001	TIERPSVÄGEN	
OBJEKTNUMMER	FASTIGHET	
	JÖRSÖN 9:4	
DISCIPLIN	FÖRETAG	
K	KÄVER & MELLIN AB	
UPPDRAGSNUMMER	SKAPAD AV	
24370	LUDVIG SUNDQVIST	
TELEFON	KONTAKTPERSON	
073-330 87 06	ANDERS HEDBERG	
BYGGNADSVÄRK		
FLUGSTAD (PM 2005)		
VÄNINGSPLAN	VÄNINGSBIL	BELOMRÅDE
SYSTEM		
24-STÅLKONSTRUKTIONER		
SPECIFIKATION		
UPPSTÄLLNING, SB01-SB02		
TEKNIKSÄTTNING	SKALA	FORMAT
UPPSTÄLLNINGAR	1:20	A1
DOCUMENTNUMMER	ÄNDRING	
K-24-6-0050-447001		

FILNAMN: