




SB03a 1:20
UPE 240
ANTAL: 1st

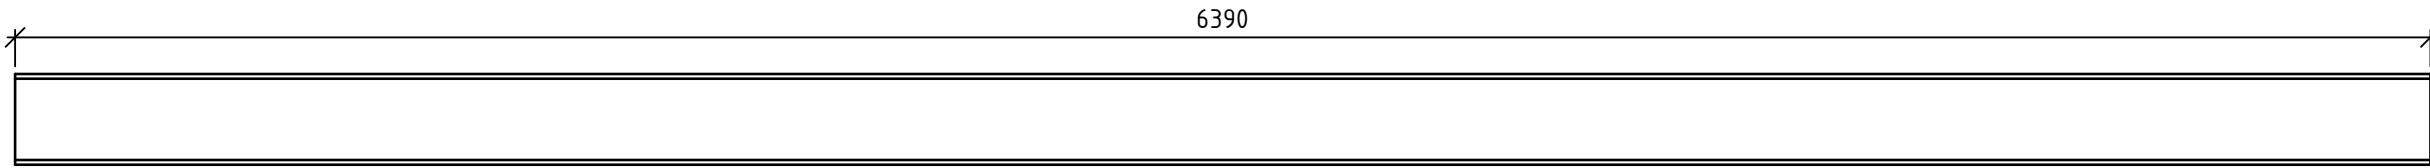


SB03b 1:20
UPE 240
ANTAL: 1st

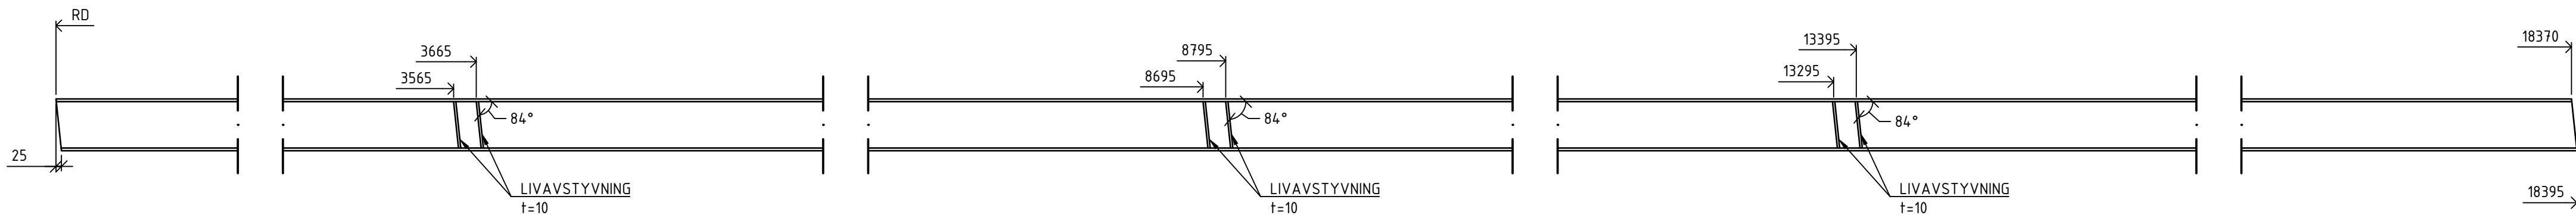


SB04 1:20
HEA 240
ANTAL: 1st

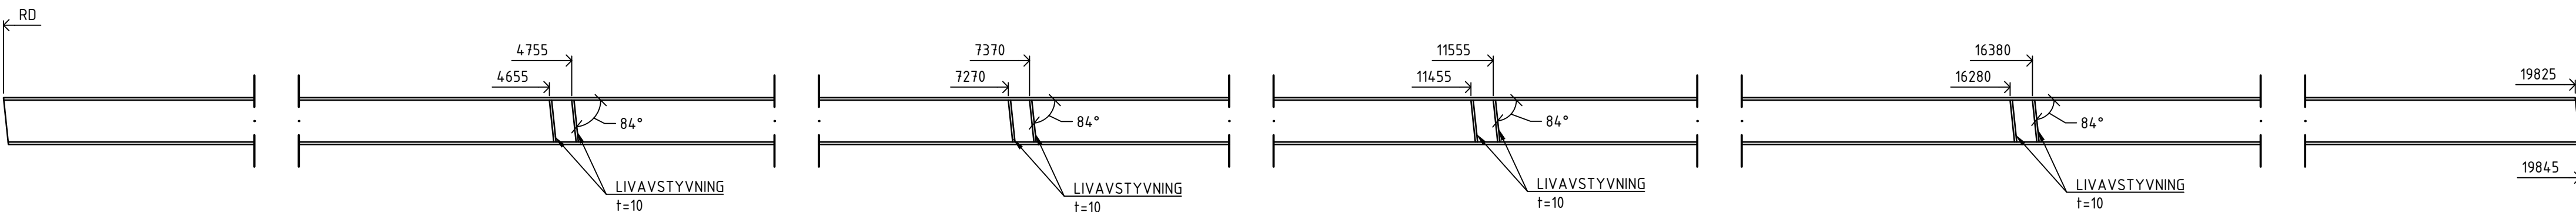


SB05 1:20
HEA 220
ANTAL: 1st

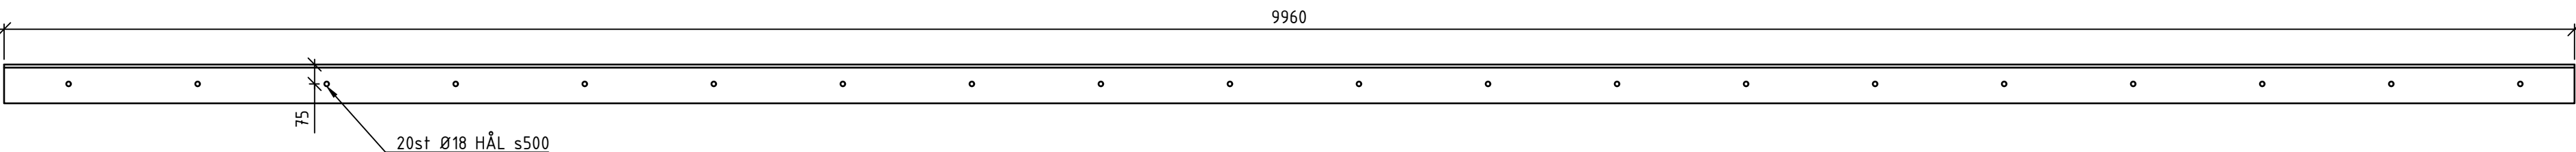


SB06a 1:20
L-STÅL 150x150x12
ANTAL: 1st

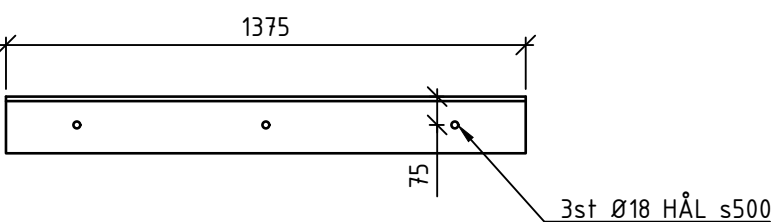

SB06b 1:20
L-STÅL 150x150x12
ANTAL: 1st

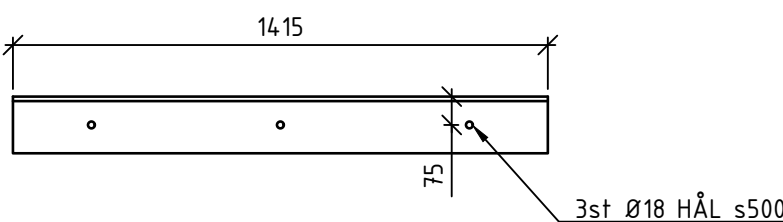

SB06c 1:20
L-STÅL 150x150x12
ANTAL: 1st

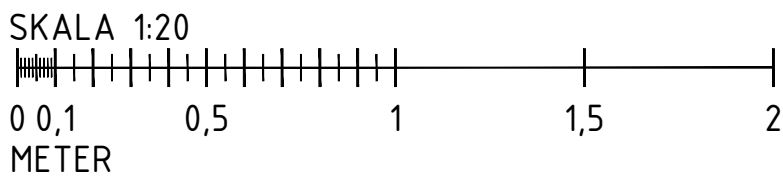

FÖRKLARINGAR

RD = UTGÅNGSPUNKT FÖR PILMÅTT

FÖRESKRIFTER

HÄNVISNINGAR

SEKTION

ORIENTERINGSGRUPP

STATUS

BYGGHANDLING

ANTAG

2026-03-27

ANSÖKAN AV

ANDERS HEDBERG

ÄNDRINGS PM

BYGGHANDLING

ANDERS HEDBERG

TIERPS

KOMMUNFASTIGHETER

PROJEKTNAMN

SÖDERFORS BRANDSTATION

OMRÅDE

TIERP SÖDERFORS

PROJEKTNUMMER

22447001

ADRESS

TIERPSVÄGEN

DIREKTOR

JÖRSÖN 9:4

DISCIPLIN

K

FORETAG

KÄVER & MELLIN AB

UPPGIFTSNUMMER

24370

BRUKAD AV

LUDVIG SUNDQVIST

TELEFON

073-330 87 06

KONTAKTPERSON

ANDERS HEDBERG

BYGGNADSVÄRK

FÖRSTÄLLNING (PM 2025)

YANINGSPLAN

YANINGSDEL

DELOMRÅDE

SYSTEM

24-STÅLKONSTRUKTIONER

SPECIFIKATION

UPPSTÄLLNING, SB03-SB06

BYGGNADSVÄRK

UPPSTÄLLNINGAR

SKALA

1:20

FORMAT

A1

BYGGNADSVÄRK

ANDERS HEDBERG

BYGGNADSVÄRK

K-24-6-0051-44 7001