




SP01a 1:20
VKR 100x100x6.3
ANTAL: 1st

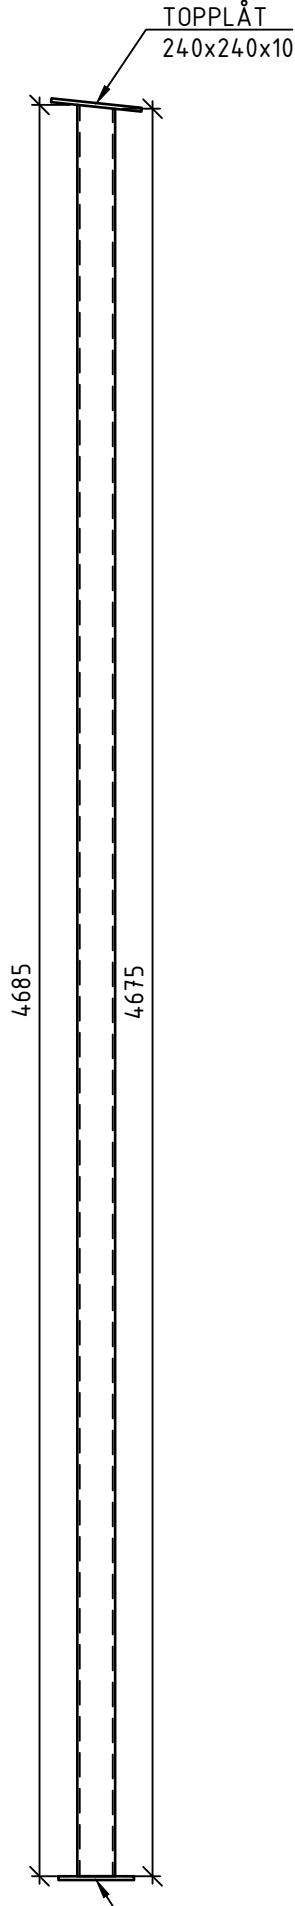


SP01b 1:20
VKR 100x100x6.3
ANTAL: 1st

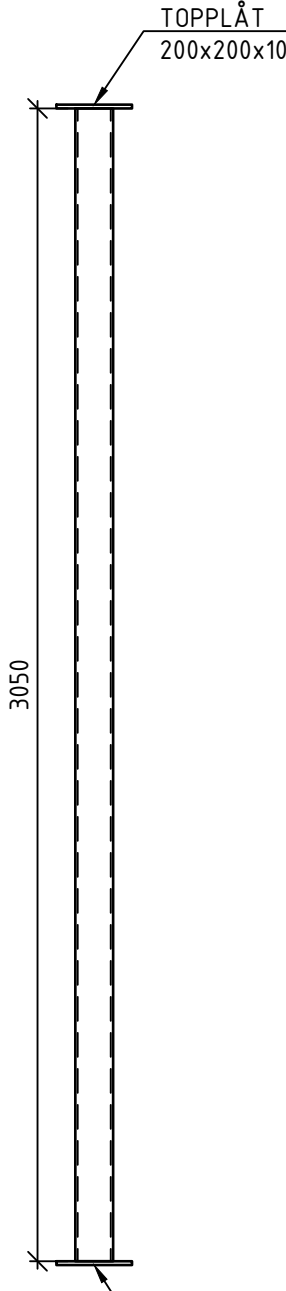


SP01c 1:20
VKR 100x100x6.3
ANTAL: 4st

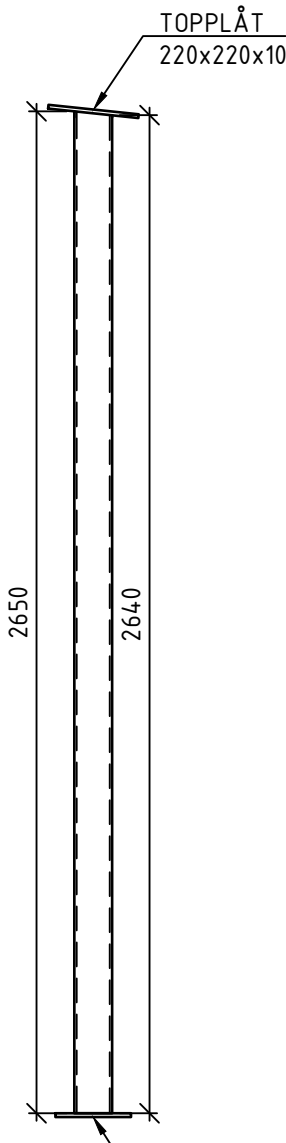


SP01d 1:20
VKR 100x100x6.3
ANTAL: 1st

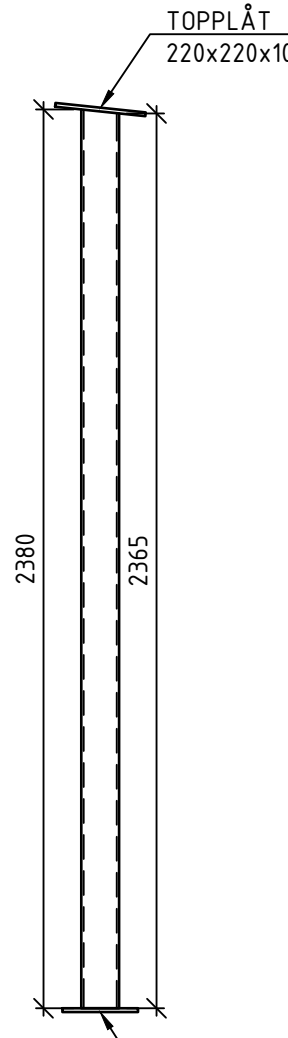

SP01e 1:20
VKR 100x100x6.3
ANTAL: 1st

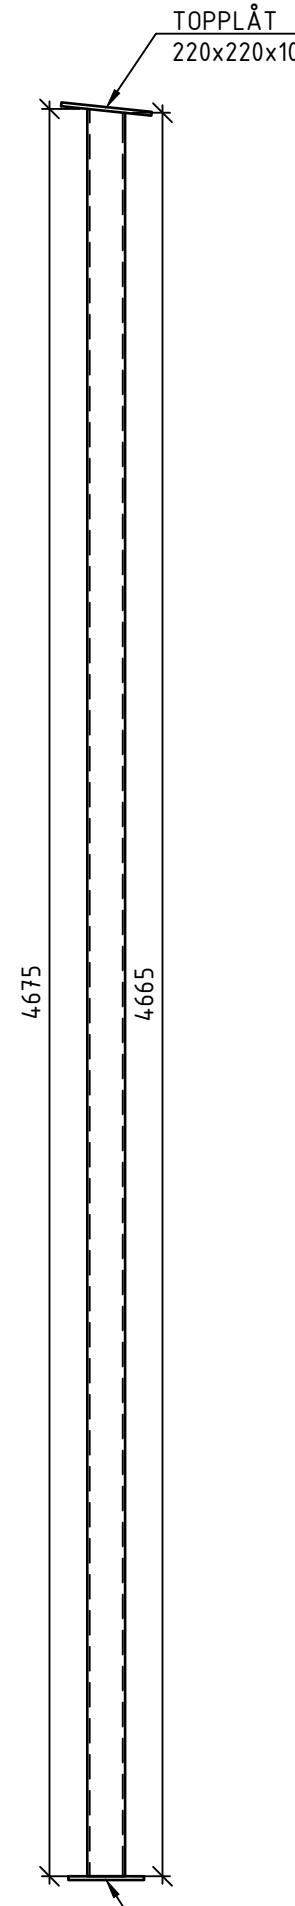

SP01f 1:20
VKR 100x100x6.3
ANTAL: 1st

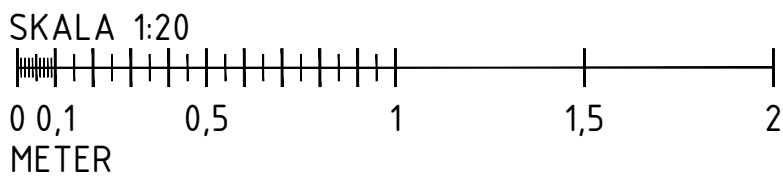

FÖRKLARINGAR

FÖRESKRIFTER

HÄNVISNINGAR

SEKTION		
ORIENTERINGSFIGUR		
STATUS		
GODKÄND		
HANDLING		
BYGGHANDLING		
ANTID	LOSRÖR	ÄNDRINGS PM
2026-03-27	ANDERS HEDBERG	
BESTÄLLARE		
PROJEKTNAMN		
SÖDERFORS BRANDSTATION		
OMRÅDE		
TIERP, SÖDERFORS		
PROJEKTNUMMER	ADRESS	
22447001	TIERPSVÄGEN	
OMRÅDE	FASTIGHET	
	JÖRSÖN 9:4	
DISCIPLIN	FÖRETAG	
K	KÄVER & MELLIN AB	
UPPDRAGSNUMMER	SKAPAD AV	
24370	LUDVIG SUNDQVIST	
TELEFON	KONTAKTPERSON	
073-330 87 06	ANDERS HEDBERG	
BYGGNADSVÄRK		
FUSIONSD (PM 2005)		
VÄNINGSPLAN	VÄNINGSBIL	BELOMRÅDE
SYSTEM		
24-STÅLKONSTRUKTIONER		
SPECIFIKATION		
UPPSTÄLLNING, SP01		
UPPSTÄLLNINGAR		SKALA
K-24-6-0052-447001		1:20
DOCUMENTNUMMER		FORMAT
		A1
		ÄNDRING