




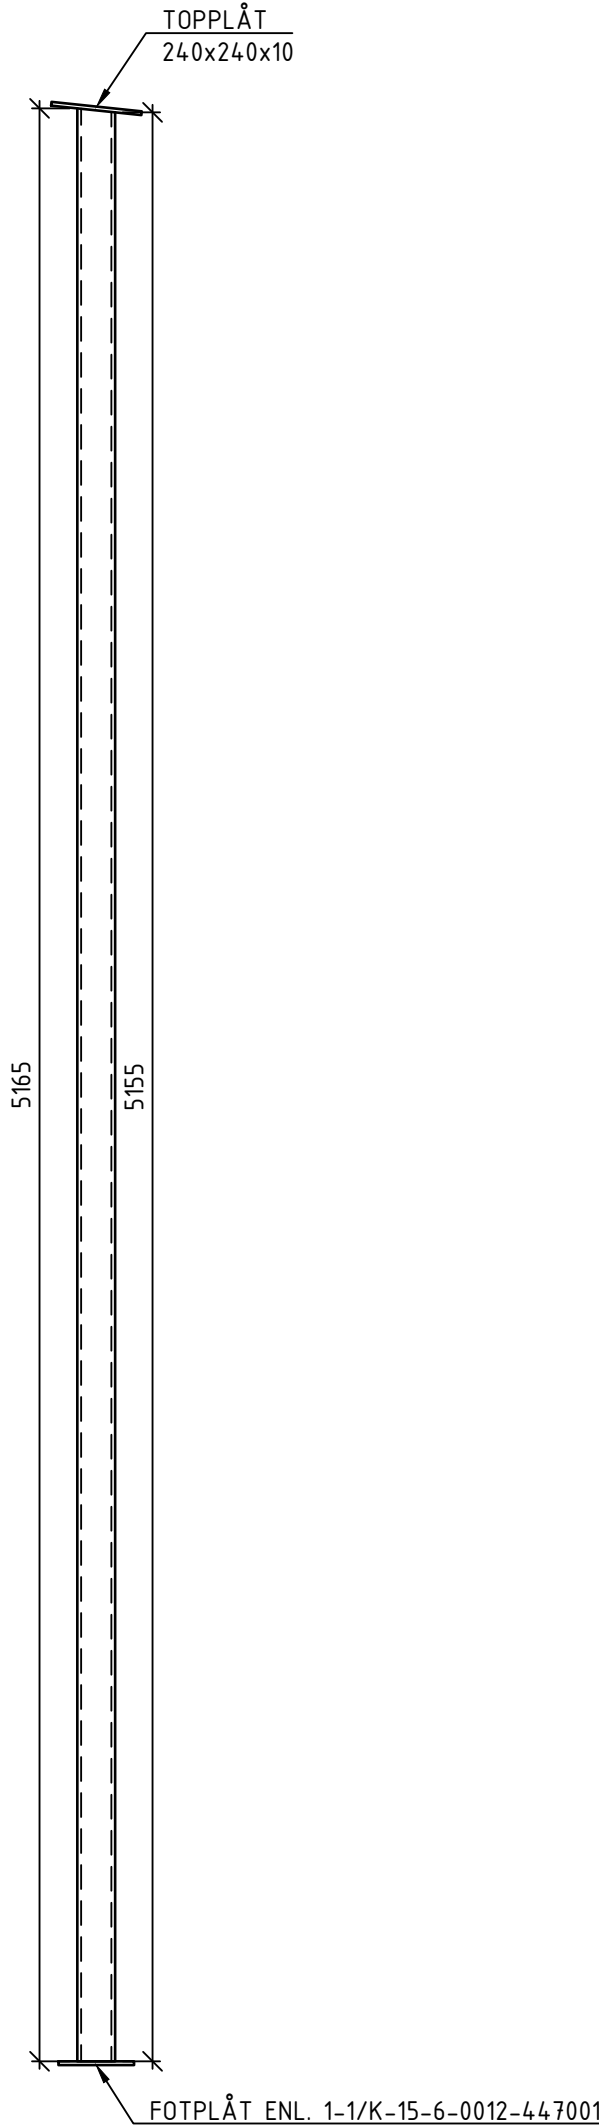


SP02a 1:20
VKR 100x100x10
ANTAL: 1st

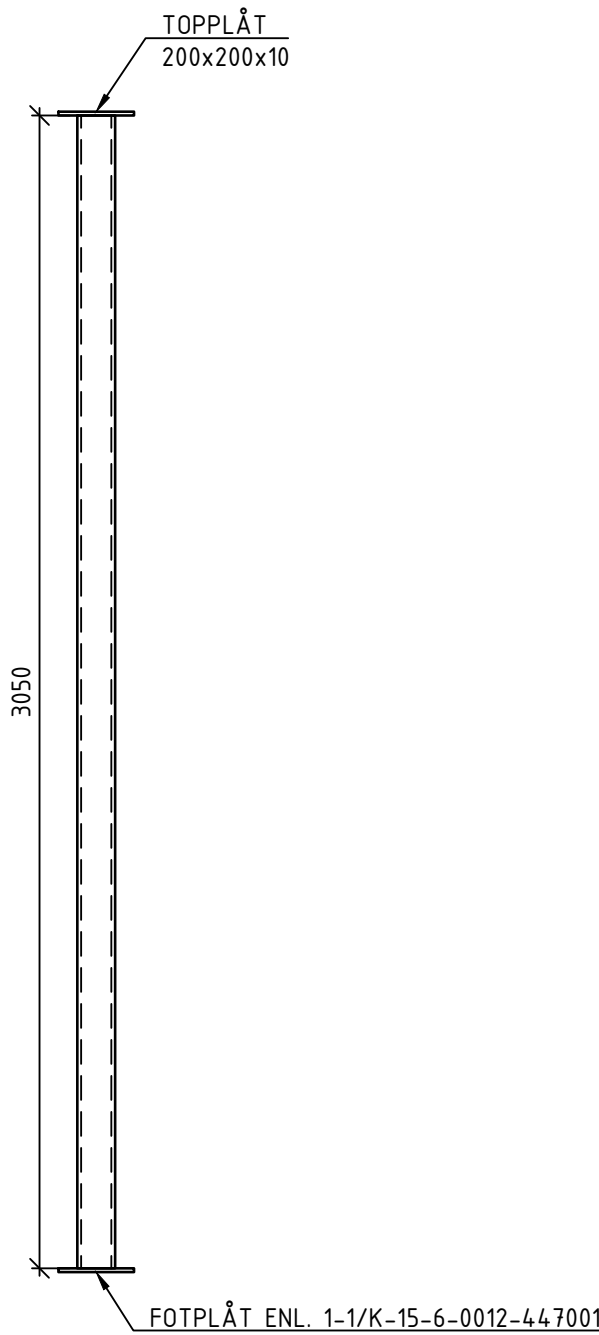

SP02b 1:20
VKR 100x100x10
ANTAL: 1st

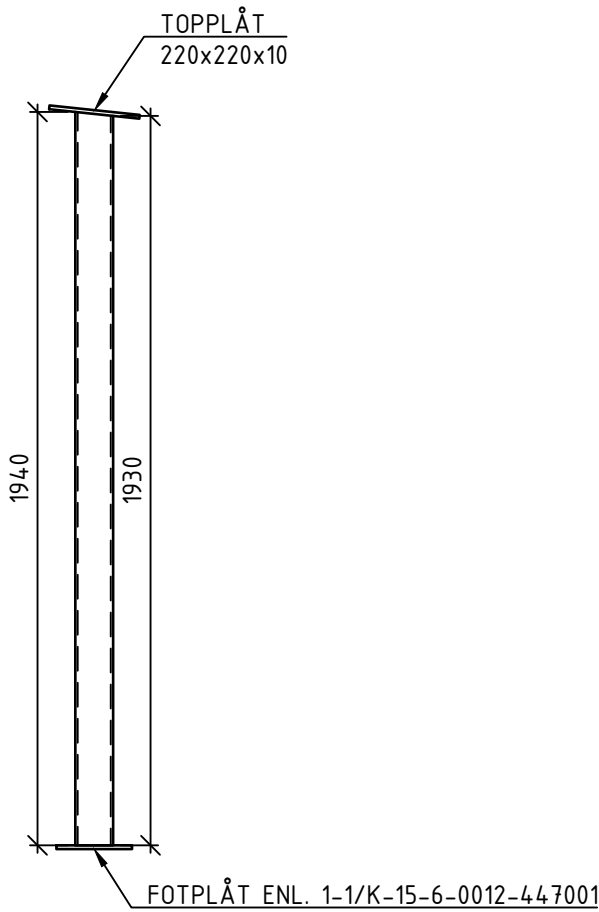

SP02c 1:20
VKR 100x100x10
ANTAL: 1st

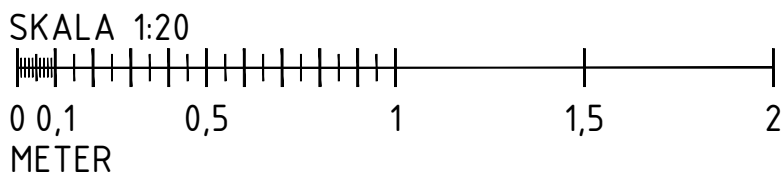

FÖRKLARINGAR

FÖRESKRIFTER

HÄNVISNINGAR

SEKTION		
ORIENTERINGSGRUPP		
STATUS		
GODKÄND		
HANDLING		
BYGGHANDLING		
ANTID	2026-03-27	ANDERS HEDBERG
BESTÄLLARE		
PROJEKTNAMN		
SÖDERFORS BRANDSTATION		
OMRÅDE		
TIERP, SÖDERFORS		
PROJEKTNUMMER	22447001	
ADRESS	TIERPSVÄGEN	
OMRÅDE	JÖRSÖN 9:4	
DISCIPLIN	K	
UPPDRAGSNUMMER	24370	
TELEFON	073-330 87 06	
BYGGNADSVÄRK	ANDERS HEDBERG	
VÄNINGSPLAN	VÄNINGSBIL	DELOMRÅDE
SYSTEM		
24-STÅLKONSTRUKTIONER		
SPECIFIKATION		
UPPSTÄLLNING, SP02		
UPPSTÄLLNINGAR		SKALA 1:20
K-24-6-0053-447001		ANDERS