



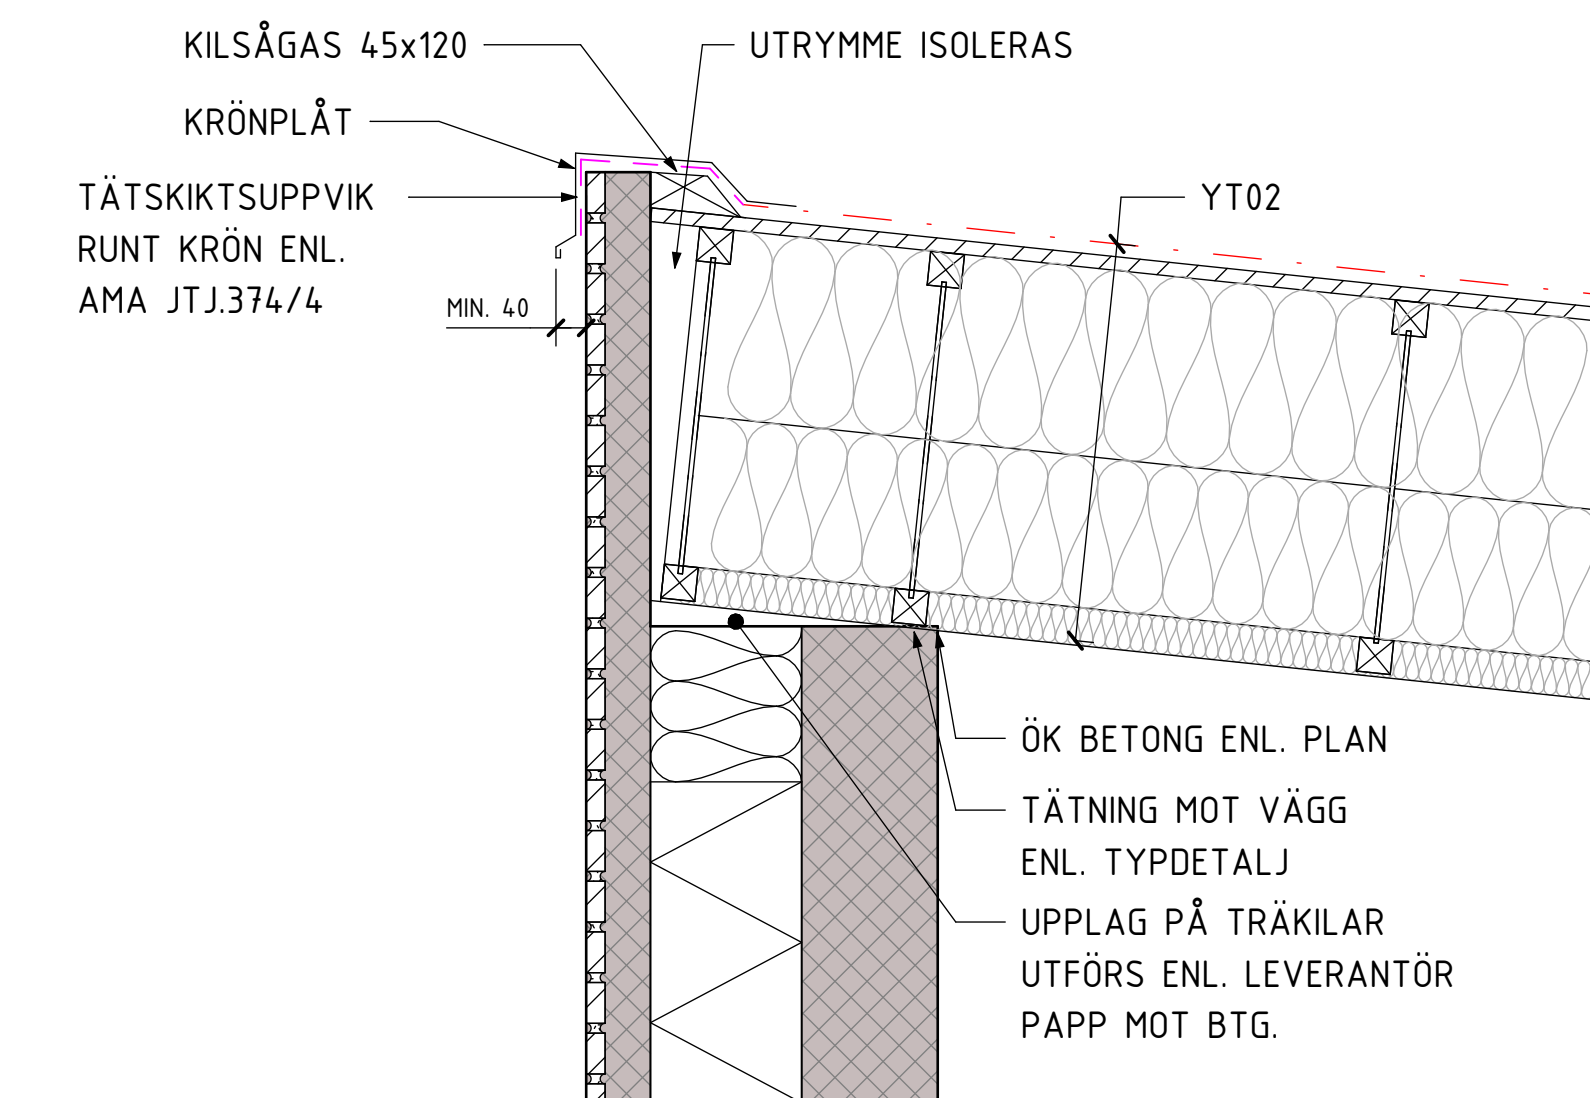


A - A ————— 1 : 10

UTFÖRANDEPRINCIP UPPLAG MOT YTTERVÄGG
ENL. LÄTTELEMENTS TYPDETALJER.
RITNING: 605, DATERAD 2025-05-15

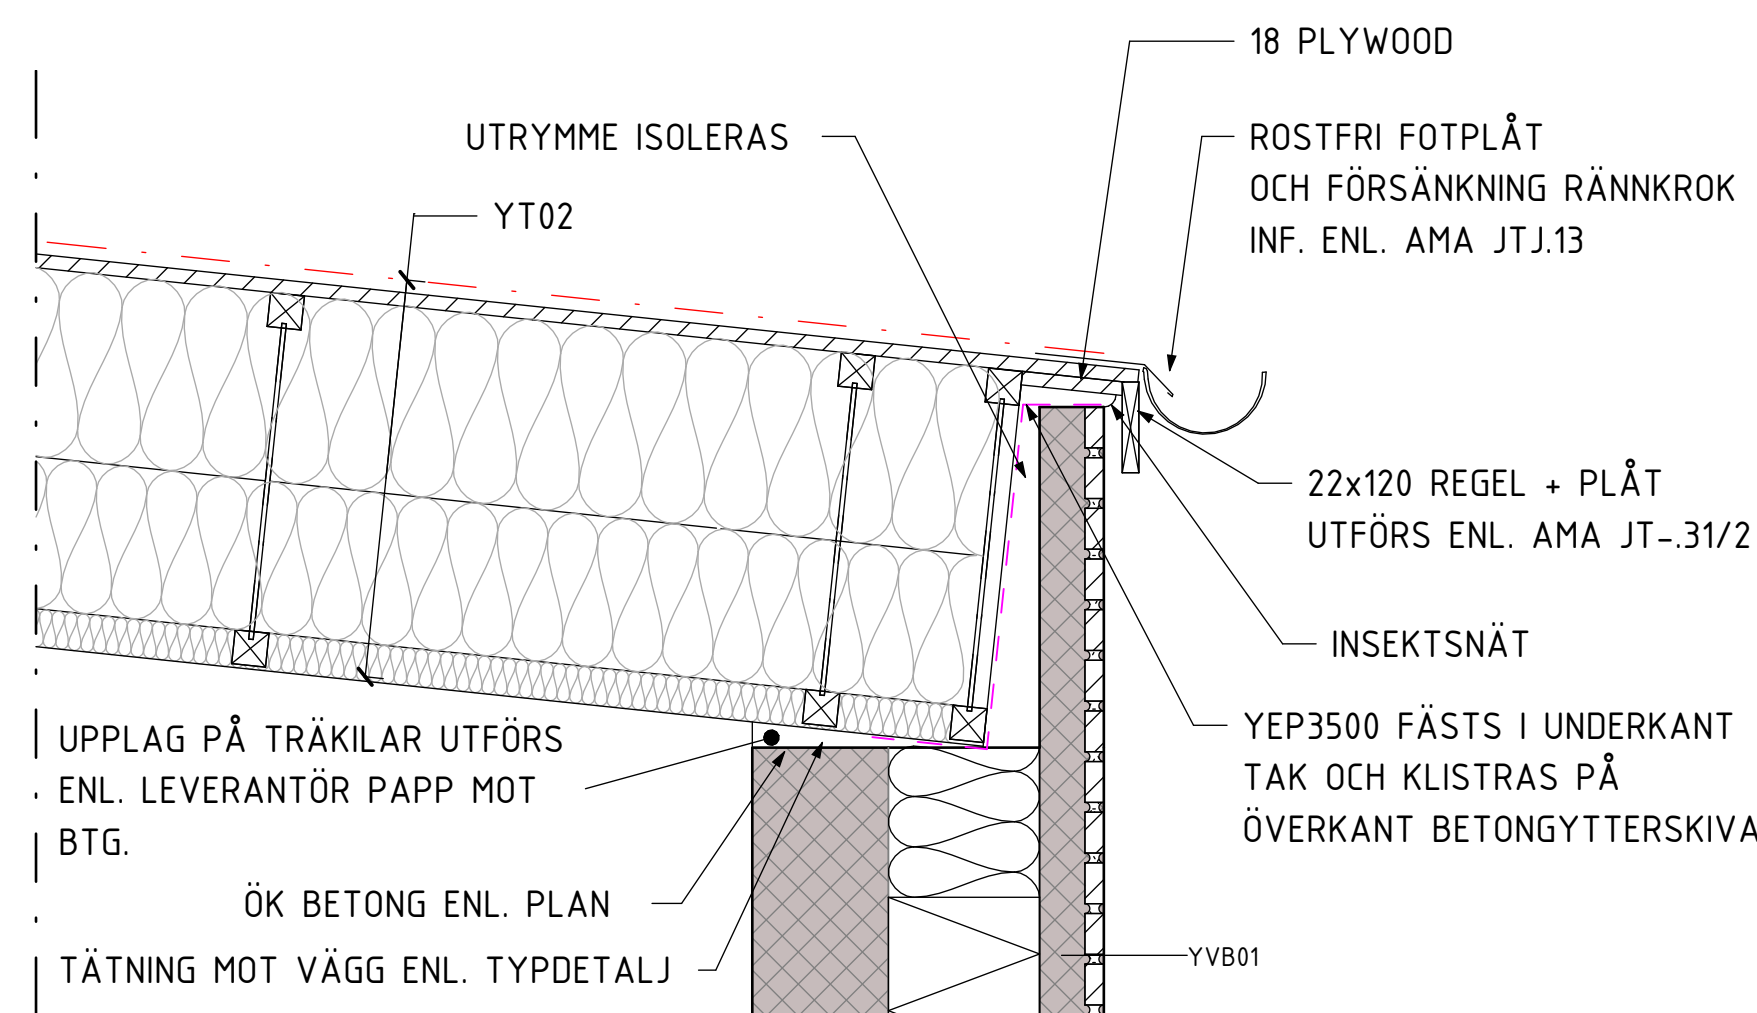


B - B ——— 1 : 10

UTFÖRANDEPRINCIP UPPLAG MOT YTTERVÄGG
ENL. LÄTTELEMENTS TYPDETALJER.
RITNING: 406. DATERAD 2025-05-15

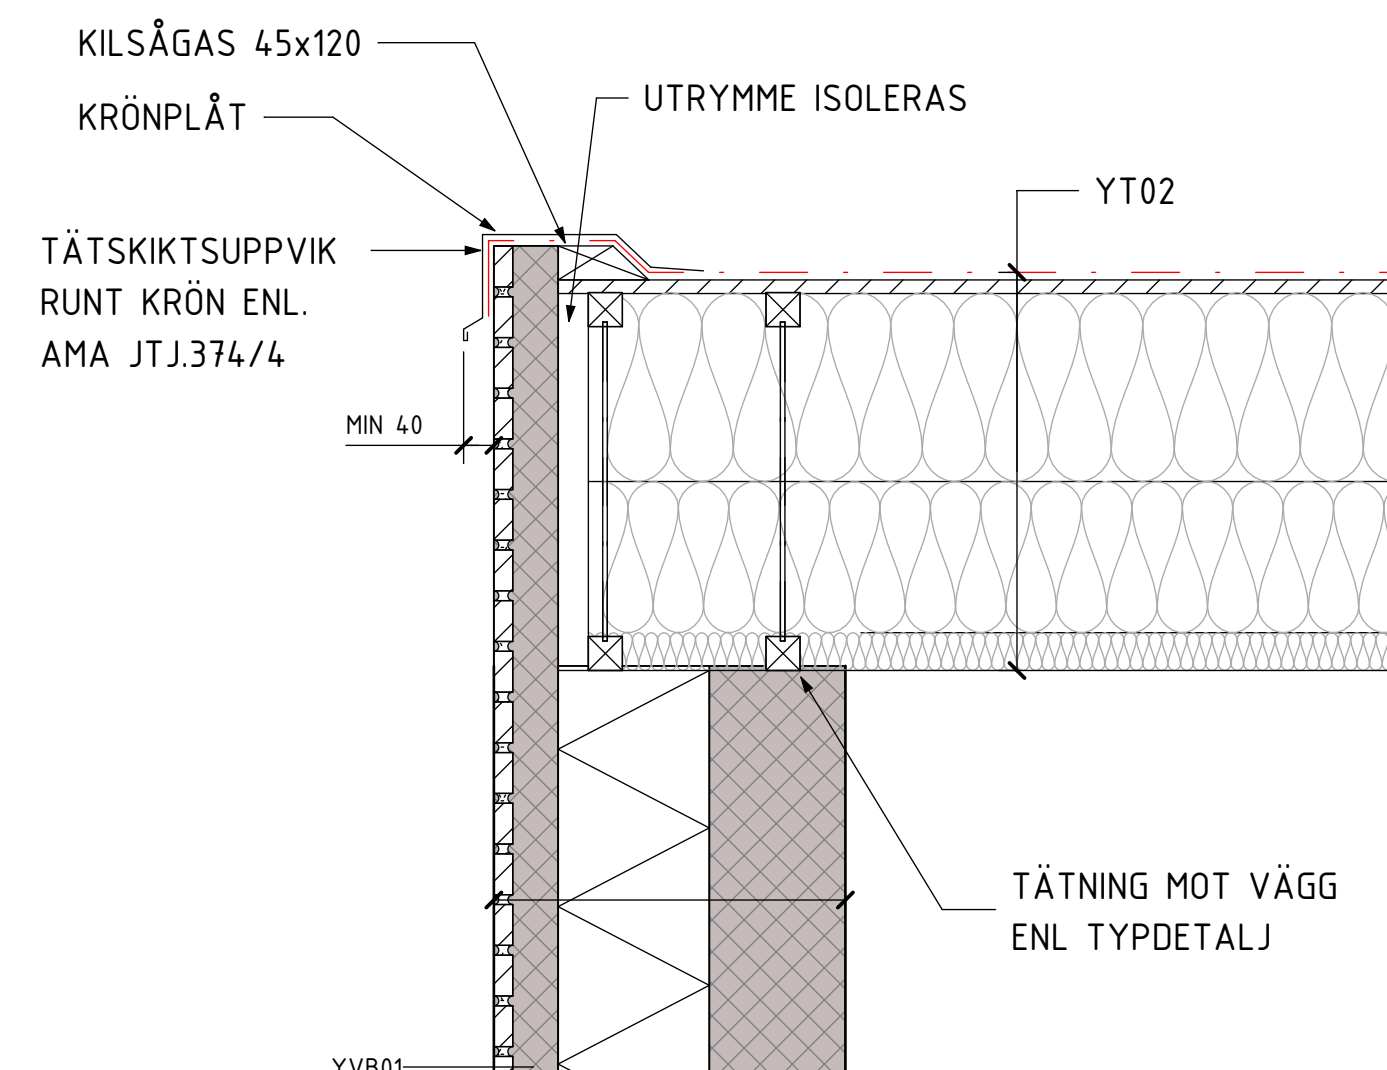


C - C ——— 1 : 10

UTFÖRANDEPRINCIP UPPLAG MOT YTTERVÄGG
ENL. LÄTTELEMENTS TYPDETALJER.
RITNING: 504, DATERAD 2025-05-15

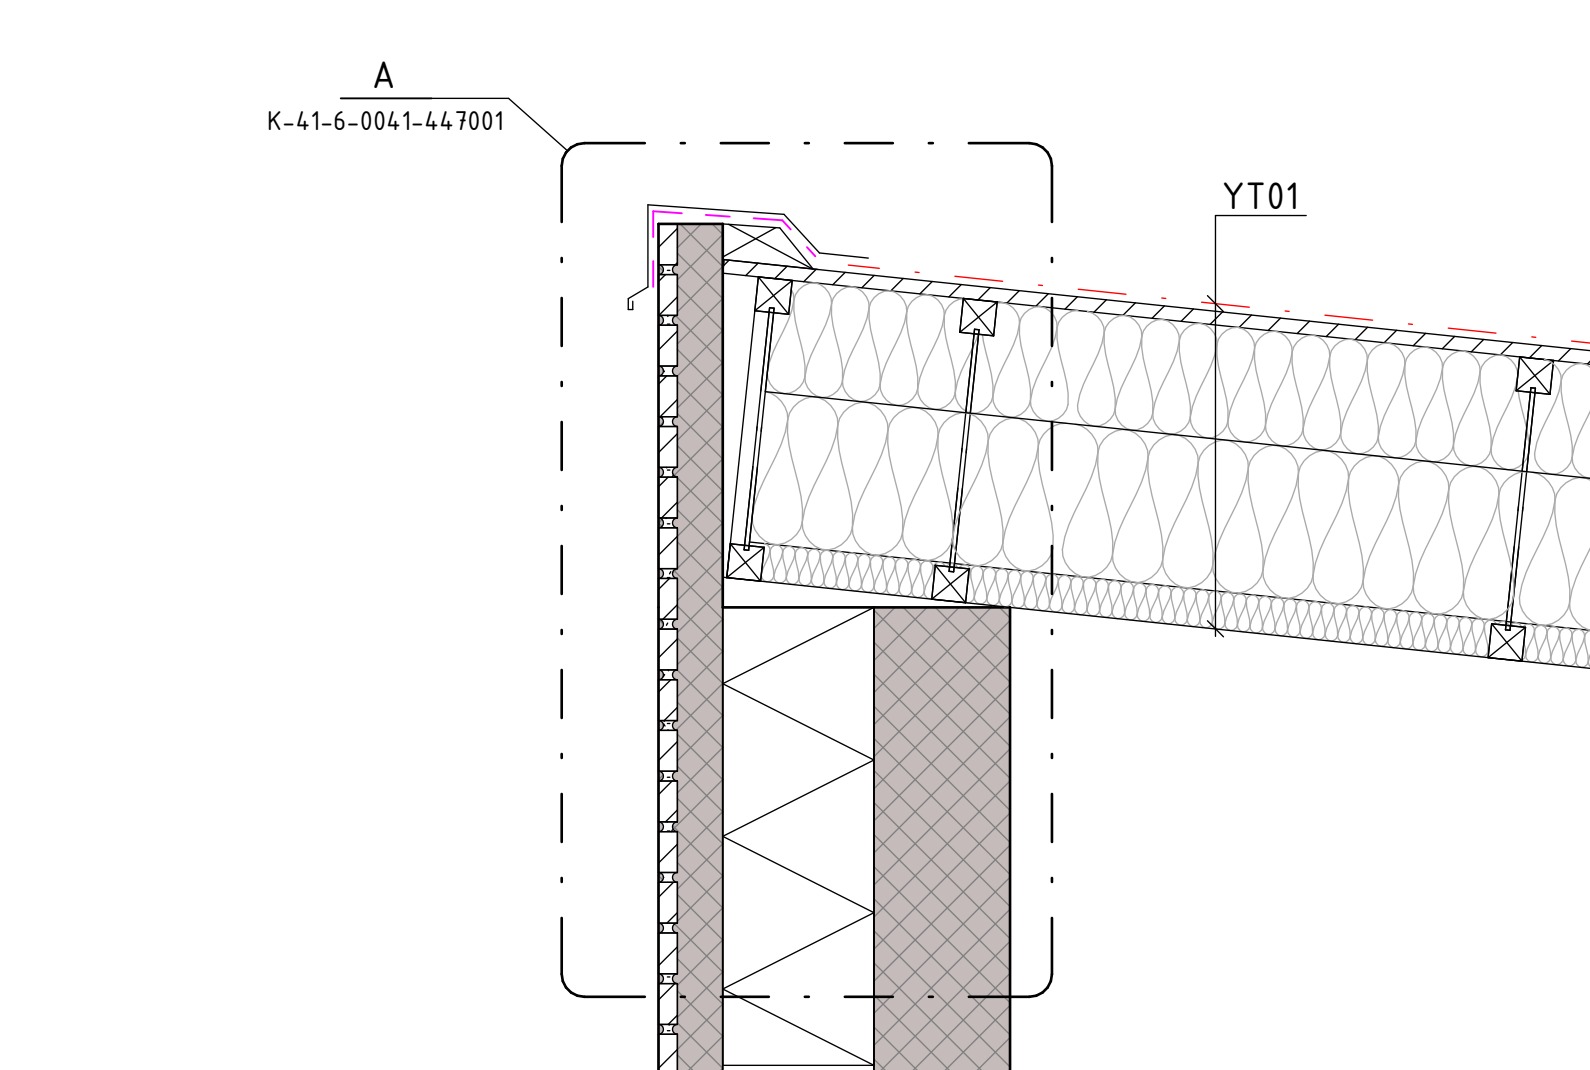


D - D ——— 1 : 10

UTFÖRANDEPRINCIP UPPLAG MOT YTTERVÄGG
ENL. LÄTTELEMENTS TYPDETALJER.
RITNING: 605, DATERAD 2025-05-15

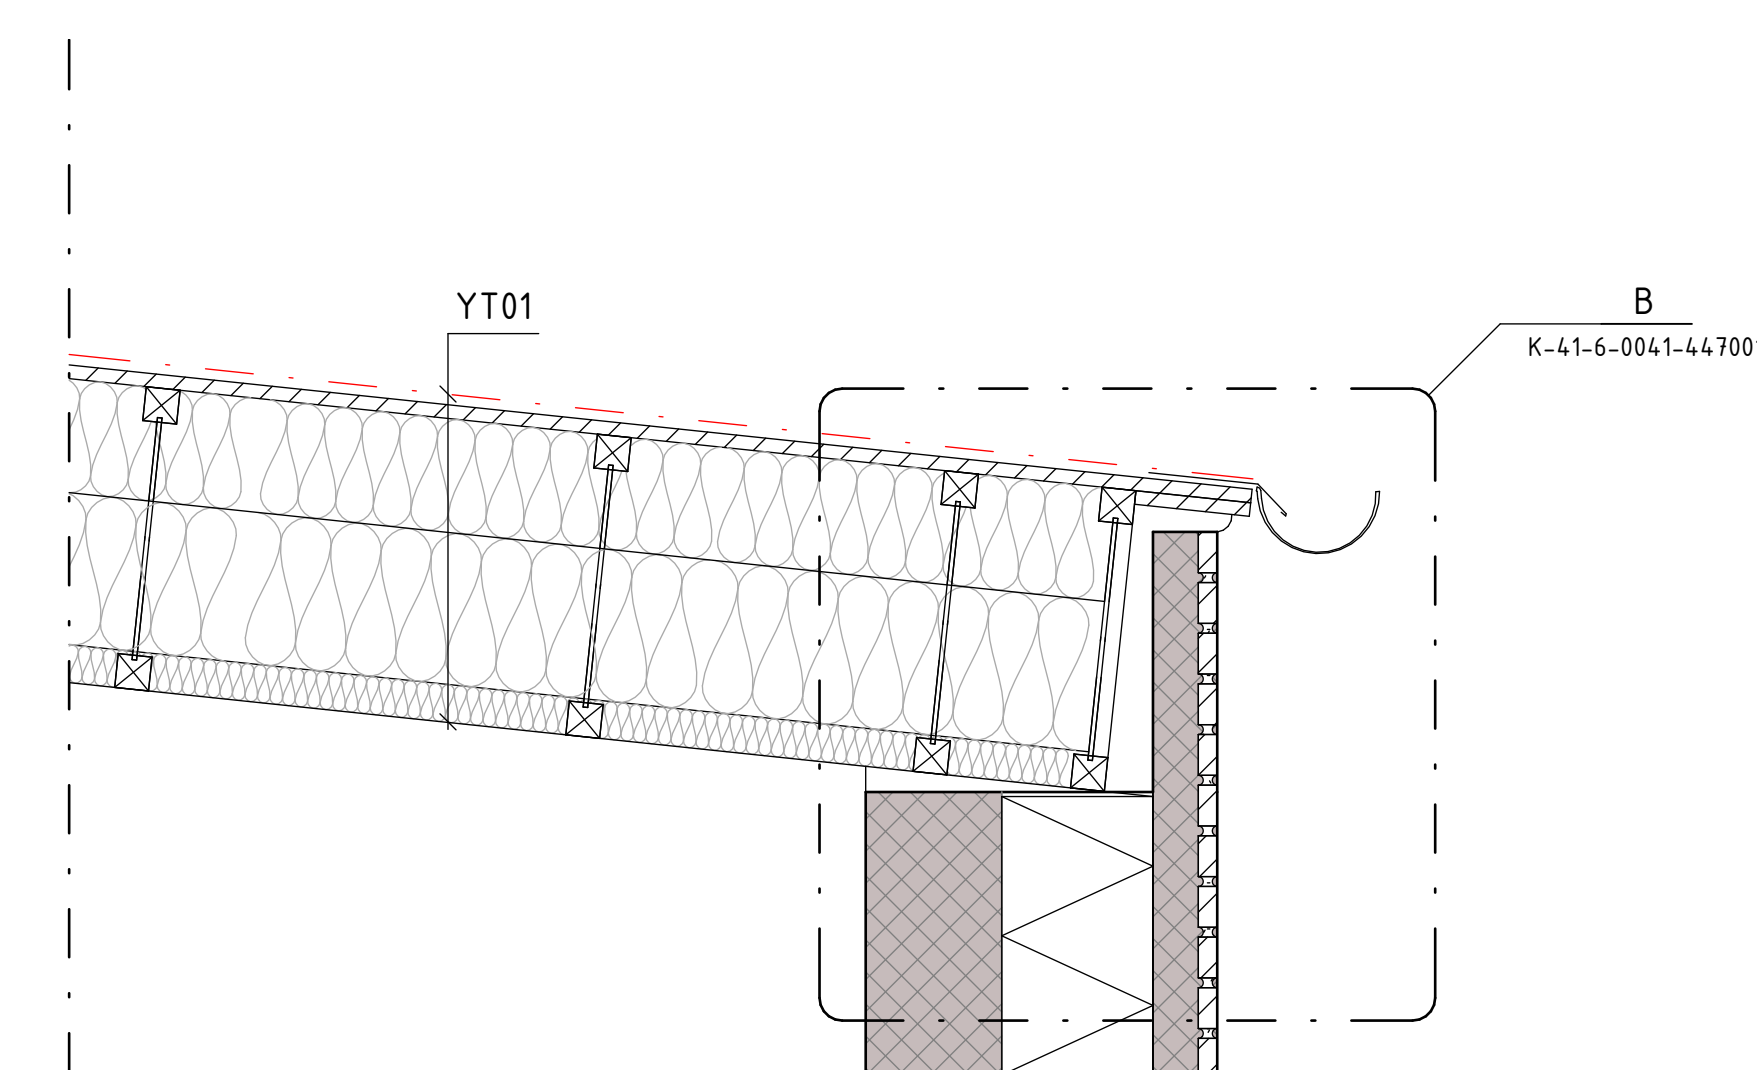


E - E ——— 1 : 10

UTFÖRANDEPRINCIP UPPLAG MOT YTTERVÄGG
ENL. LÄTTELEMENTS TYPDETALJER.
RITNING: 406, DATERAD 2025-05-15

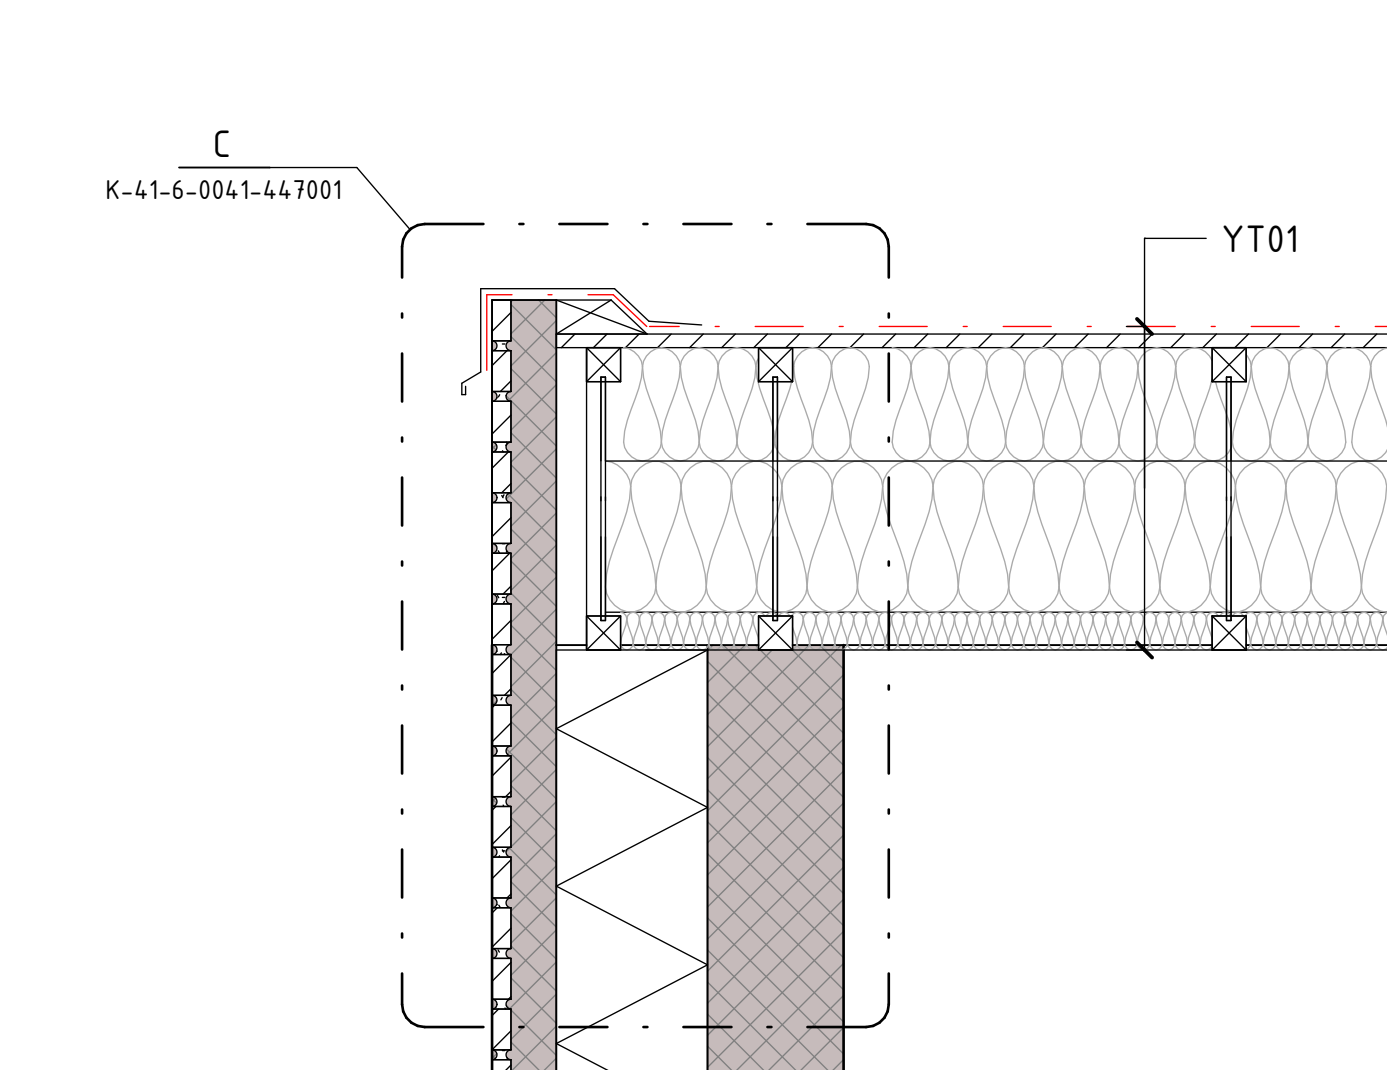


F - F ——— 1 : 10

UTFÖRANDEPRINCIP UPPLAG MOT YTTERVÄGG
ENL. LÄTTELEMENTS TYPDETALJER.
RITNING: 504, DATERAD 2025-05-15

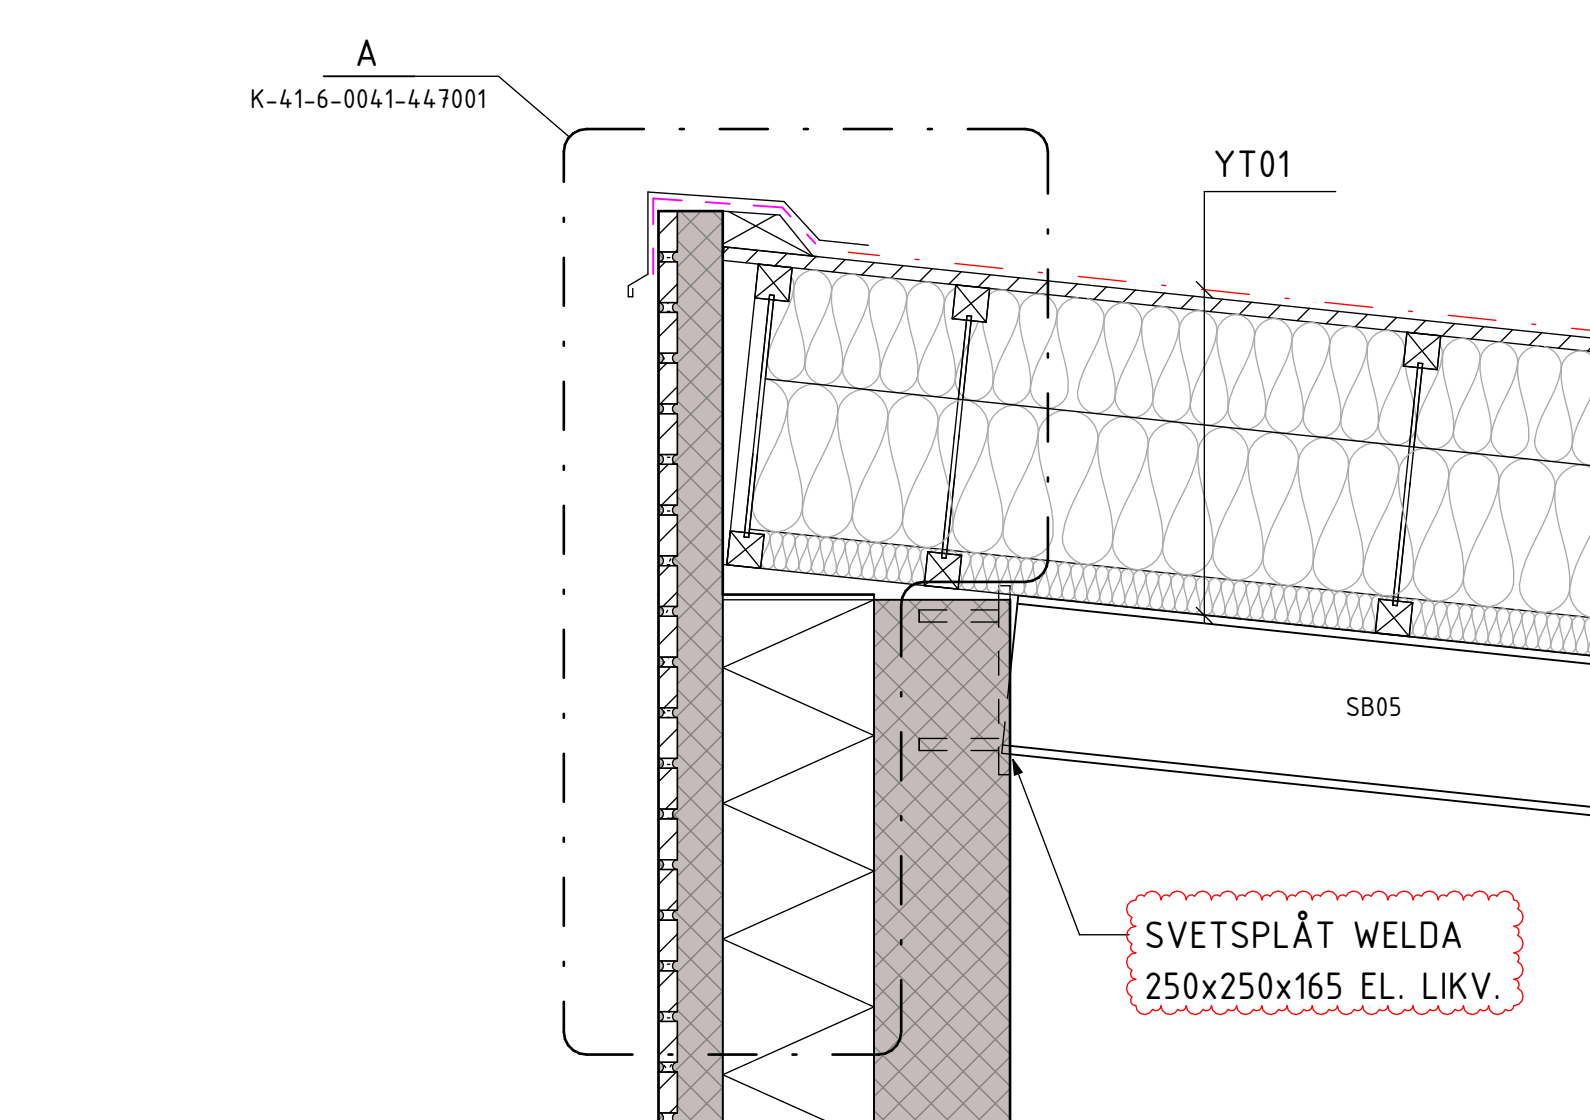

G - G — 1 : 10

UTFÖRANDEPRINCIP UPPLAG MOT YTTERVÄGG
ENL. LÄTTELEMENTS TYPDETALJER.
RITNING: 605, DATERAD 2025-05-15

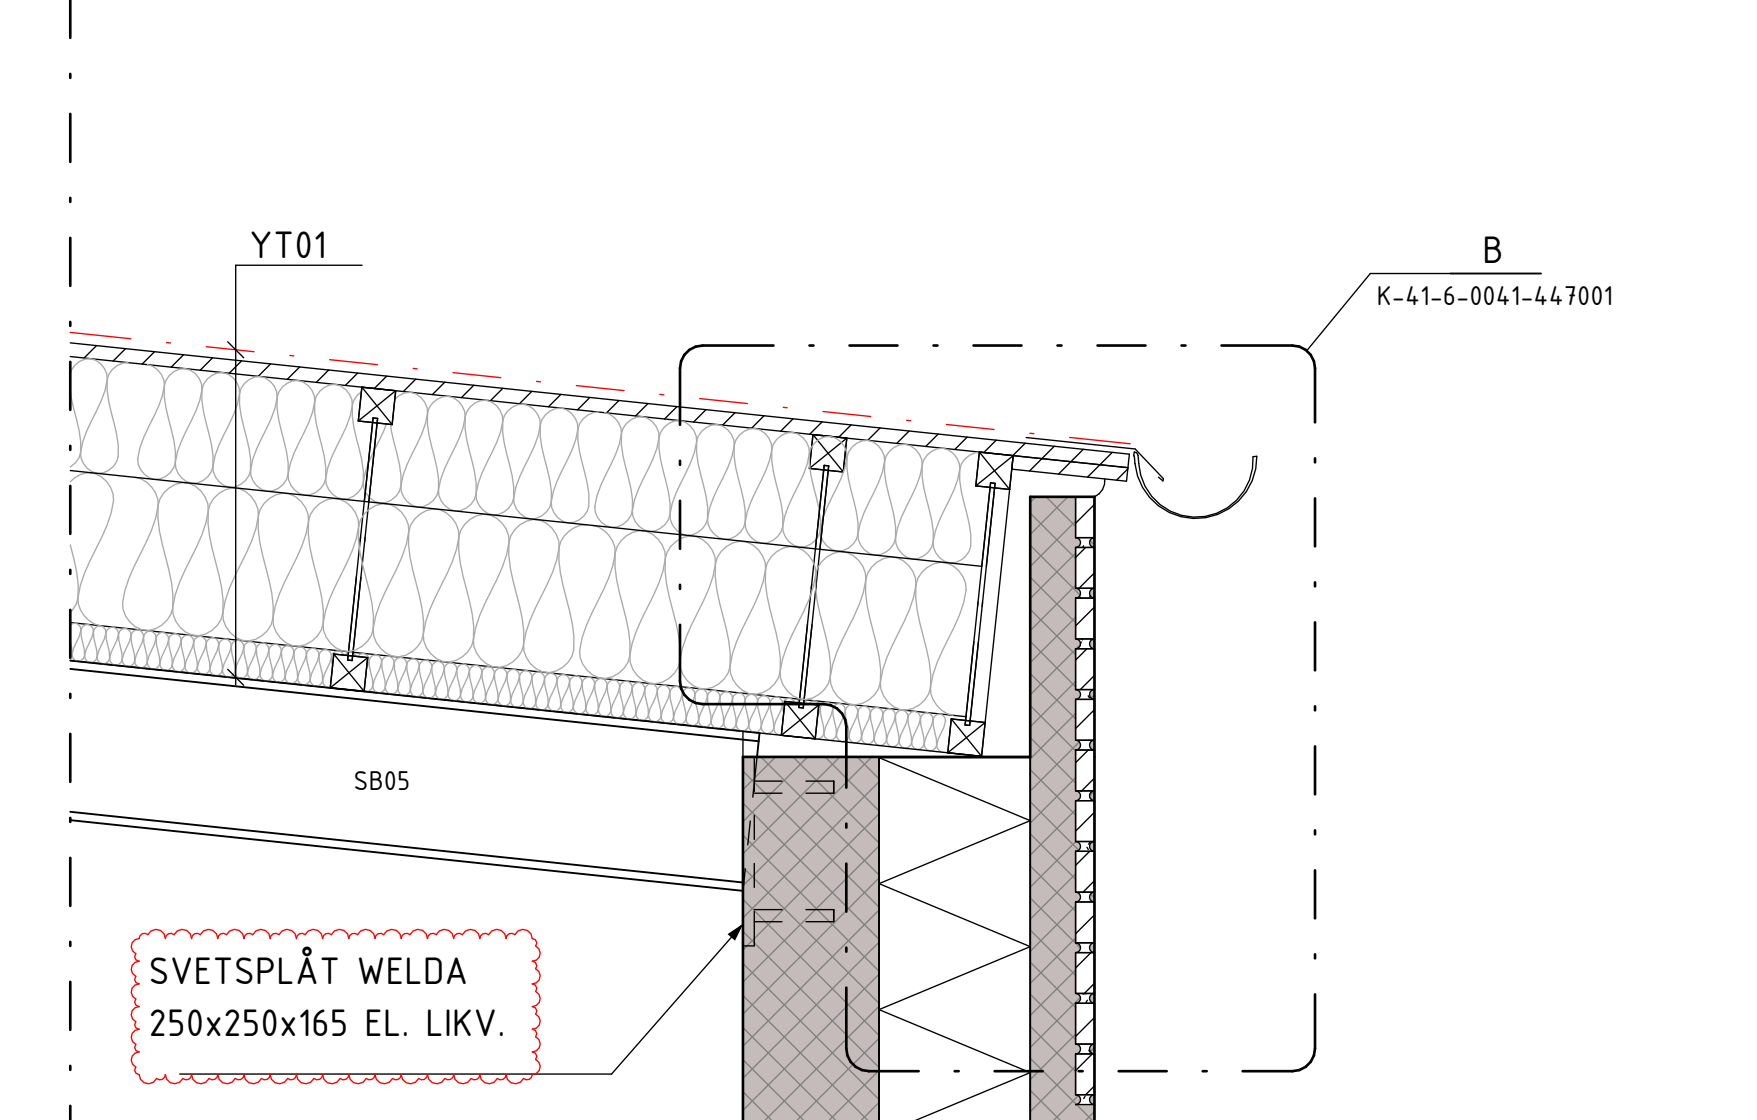
$$\text{H} - \text{H} \text{ ————— } 1 : 10$$



UTFÖRANDEPRINCIP UPPLAG MOT YTTERVÄGG
ENL. LÄTTELEMENTS TYPDETALJER.
RITNING: 406, DATERAD 2025-05-15

YT= YTTERTAK
YVB = YTTERVÄGG BÄRANDE
SP= STÅLPELARE

VÄGG- & BJÄLKLAGSTYPER	K-20-6-0020-447001
TAKPLANER	K-41-1-0300-447001
TAKTYPER	K-41-6-0040-447001

A	K-PM02	2026-03-27	LS
BET	ÄNDRINGEN AVSER	DATUM	SIGN

SECTION

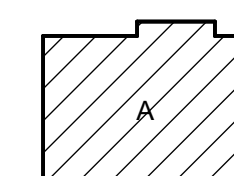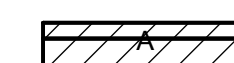

STATUS	GODKÄND
--------	---------

HANDLING	BYGGHANDLING
----------	--------------

DATUM	GODKÄND AV	ÄNDRINGS PM
2025-12-12	ANDERS HEDBERG	

BESTALLARE

TIERPS 
KOMMUNFASTIGHETER

PROJEKTNAMN
SÖDERFORS BRANDSTATION

OMRÅDE
TIERP SÖDERFORS

PROJEKTNUMMER 22447001	ADRESS TIERPSVÄGEN
---------------------------	-----------------------

DIARIENUMMER	FASTIGHET JÖRSÖN 9:4
DISCIPLIN	FÖRETAG

K	KAVER OCH MELLIN AB
UPPDRAGSNUMMER 24370	SKAPAD AV SOFIA THURESSON

TELEFON	KONTAKTPERSON
073-330 87 06	ANDERS HEDBERG

BYGGNADSVÄRK	PLUSHÖJD (Rm 2020)
--------------	--------------------

VARI033FDAN	VARI033DEL	DELORIPADE
SYSTEM		

41-YITERTAK

RITNINGSKATEGORI	SKALA	FORMAT
DETALJ	1:10	A1

DOKUMENTNUMMER	ÄNDRING
K-41-6-0041-447001	A
