




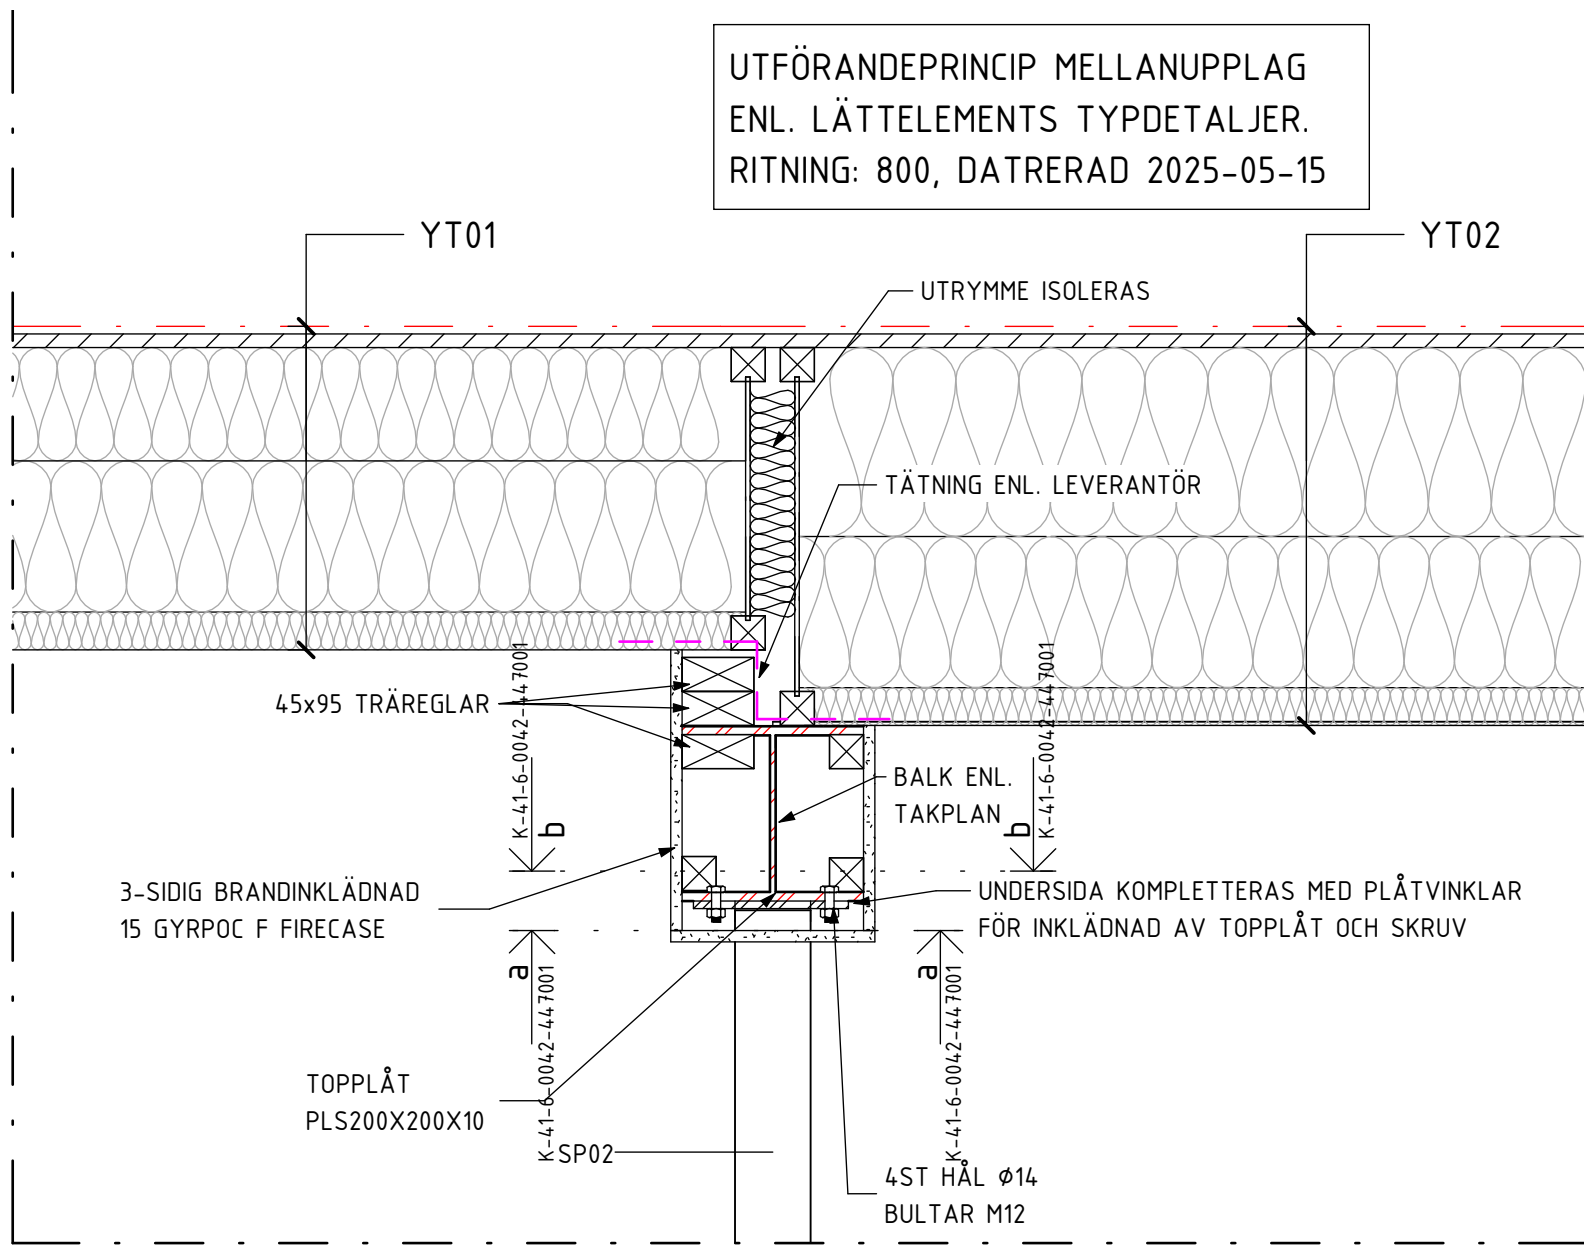


A - A 1 : 10

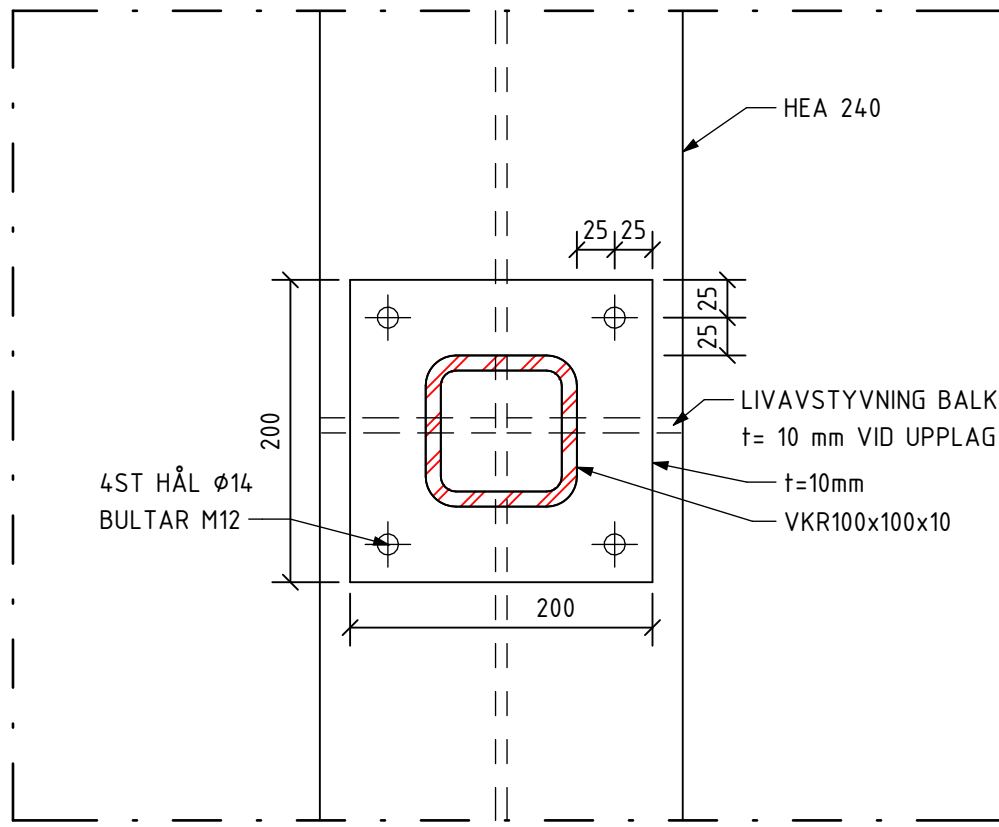


a - a 1 : 5

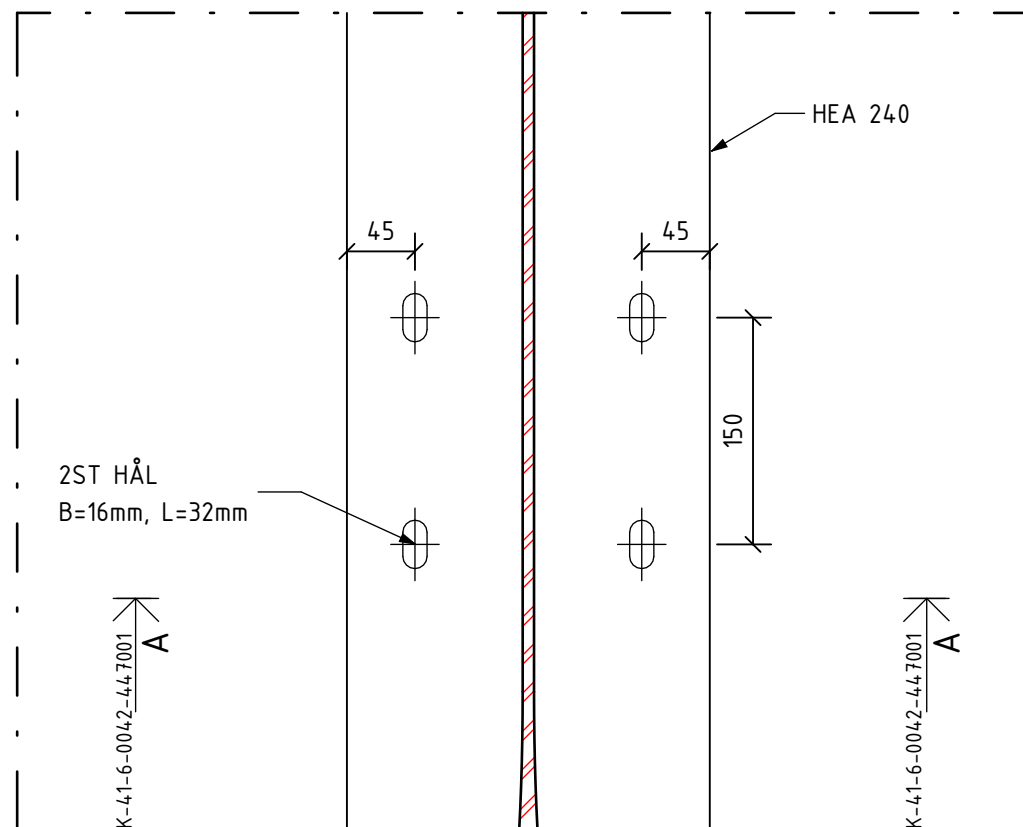

b - b 1 : 5

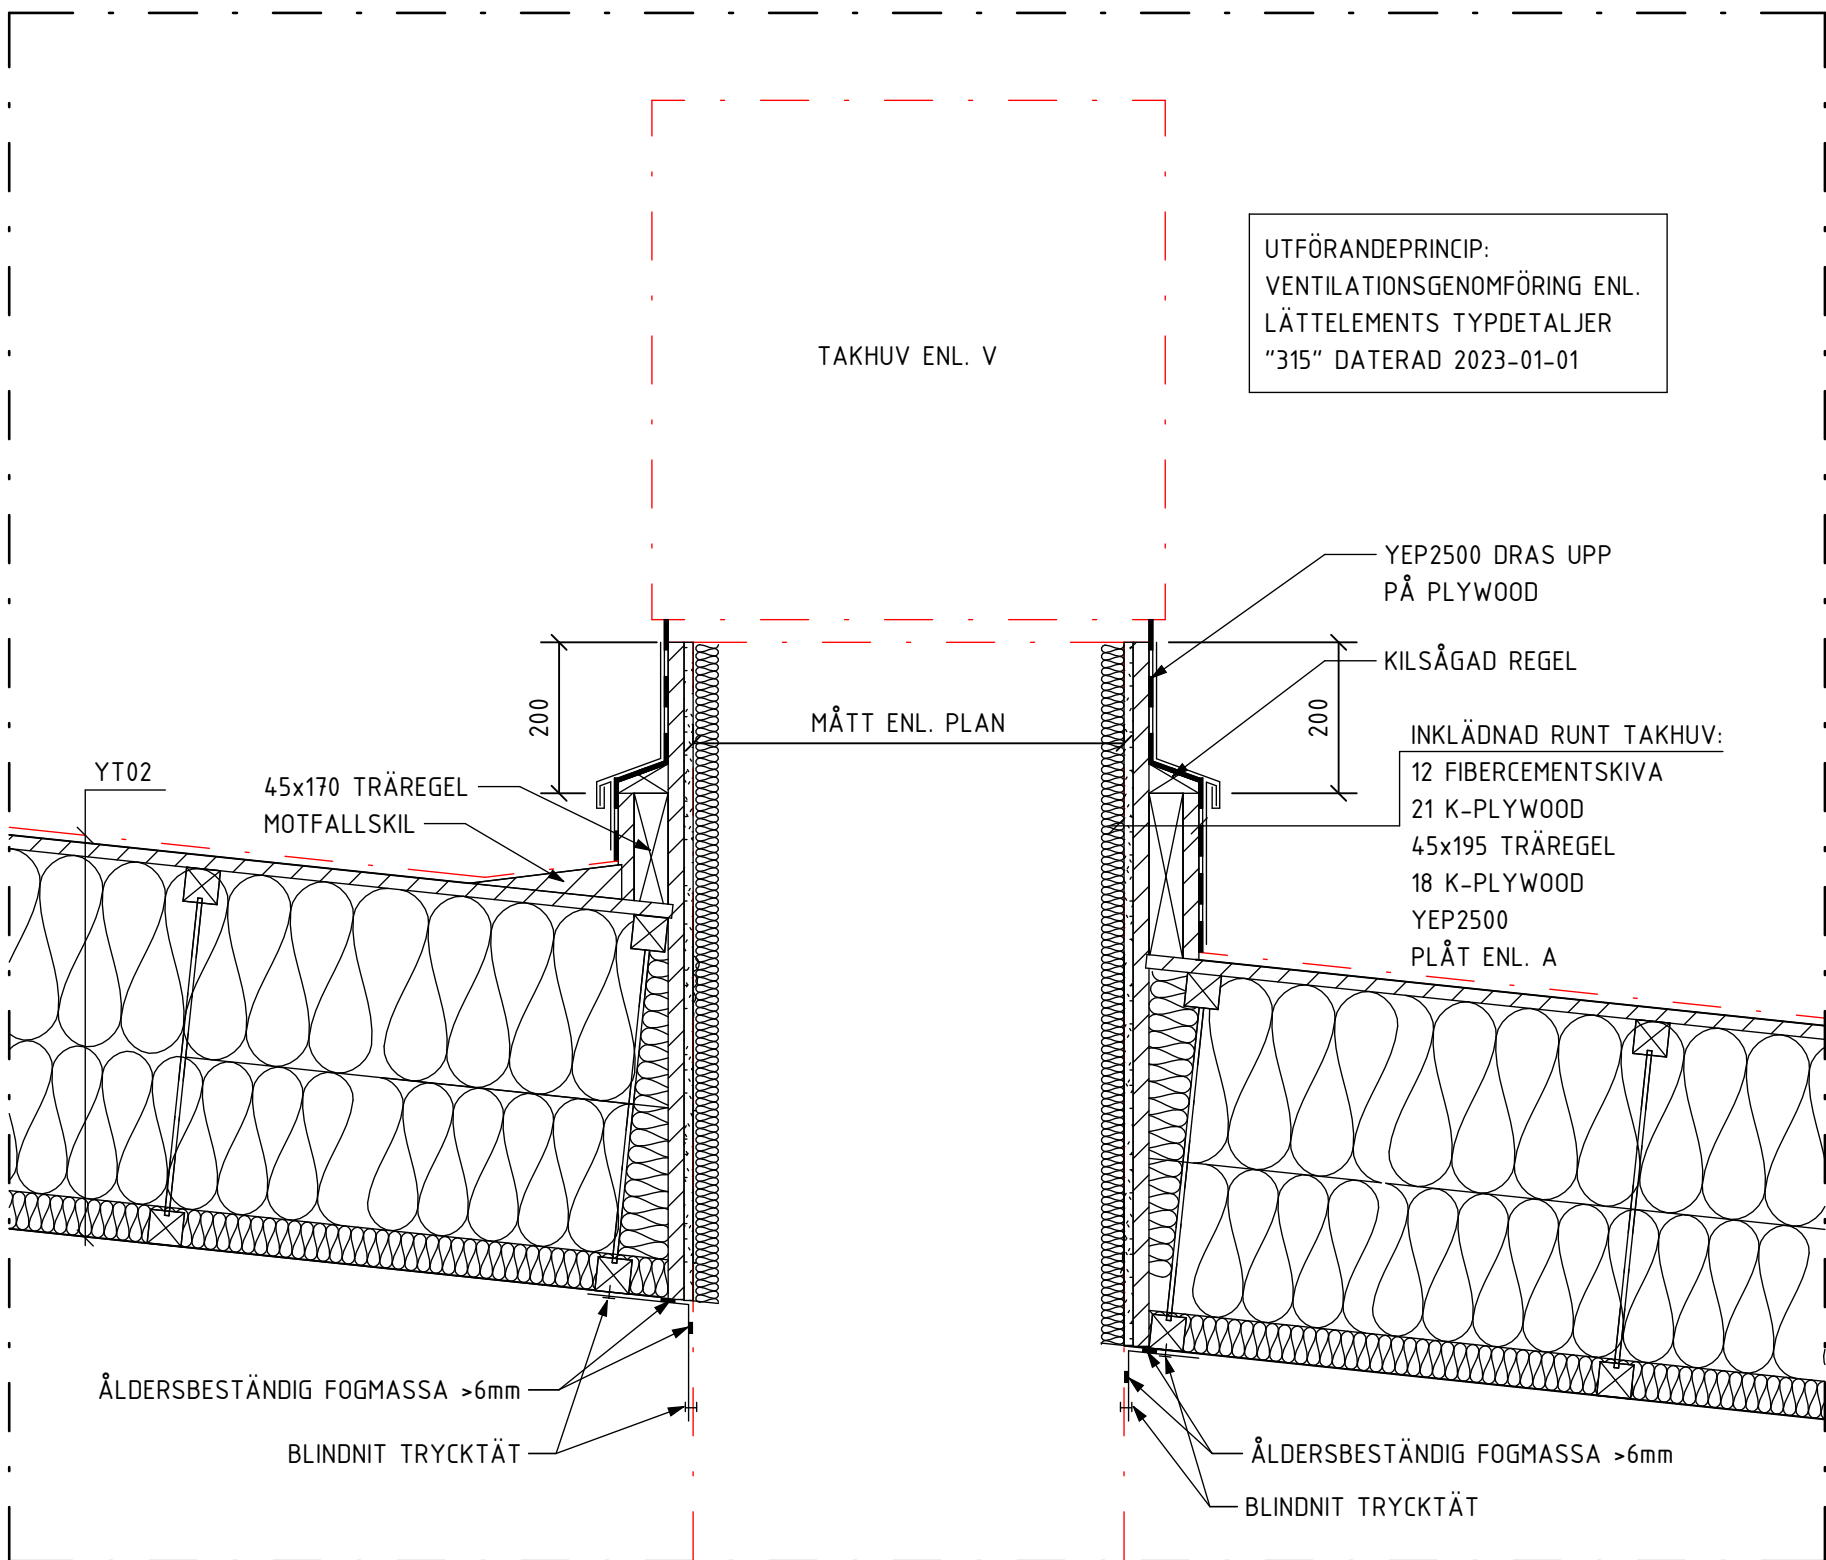


B - B 1 : 10

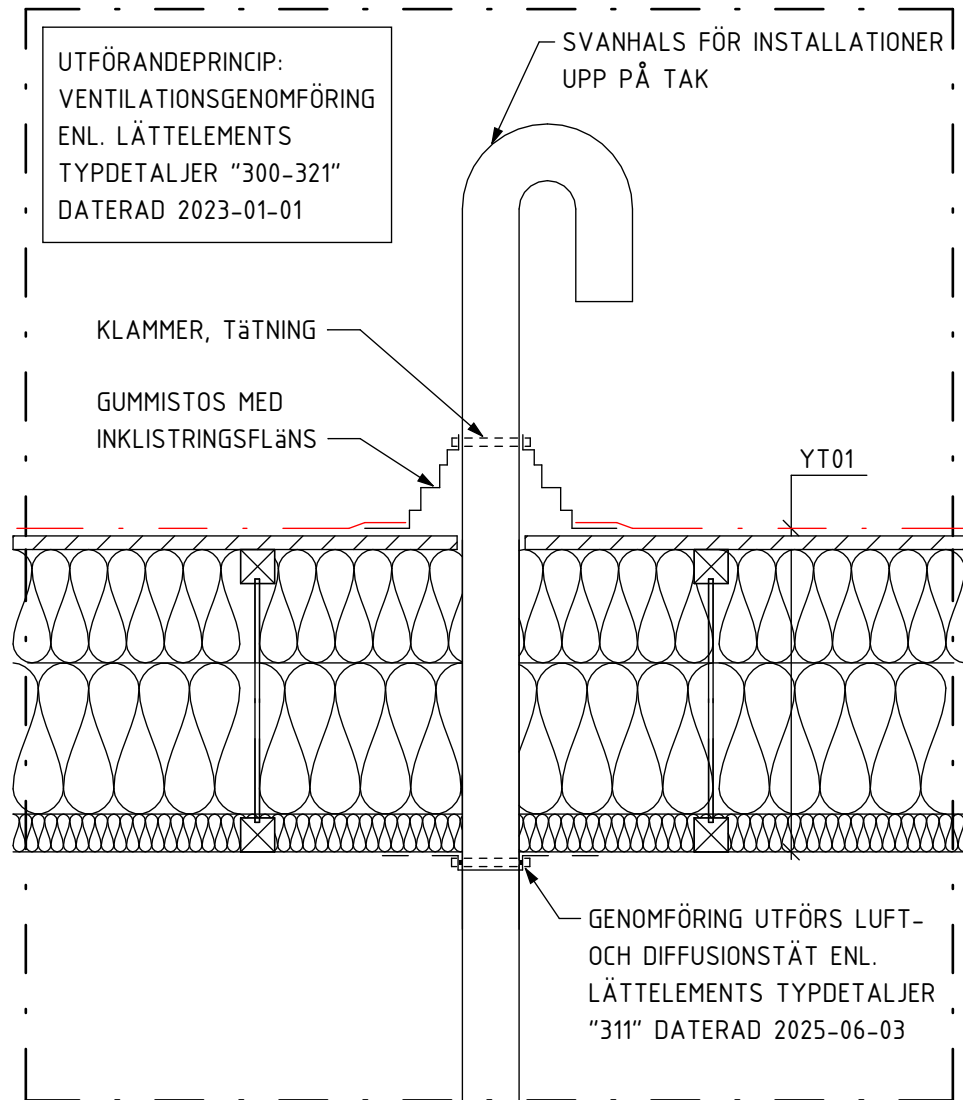

PRINCIPDETALJ 1:10


PRINCIPDETALJ SVANHALS -
RÖRUPPSTICK INSTALLATIONER PÅ TAK
TAK I VAGNHallen MED LJUDREDUKTION

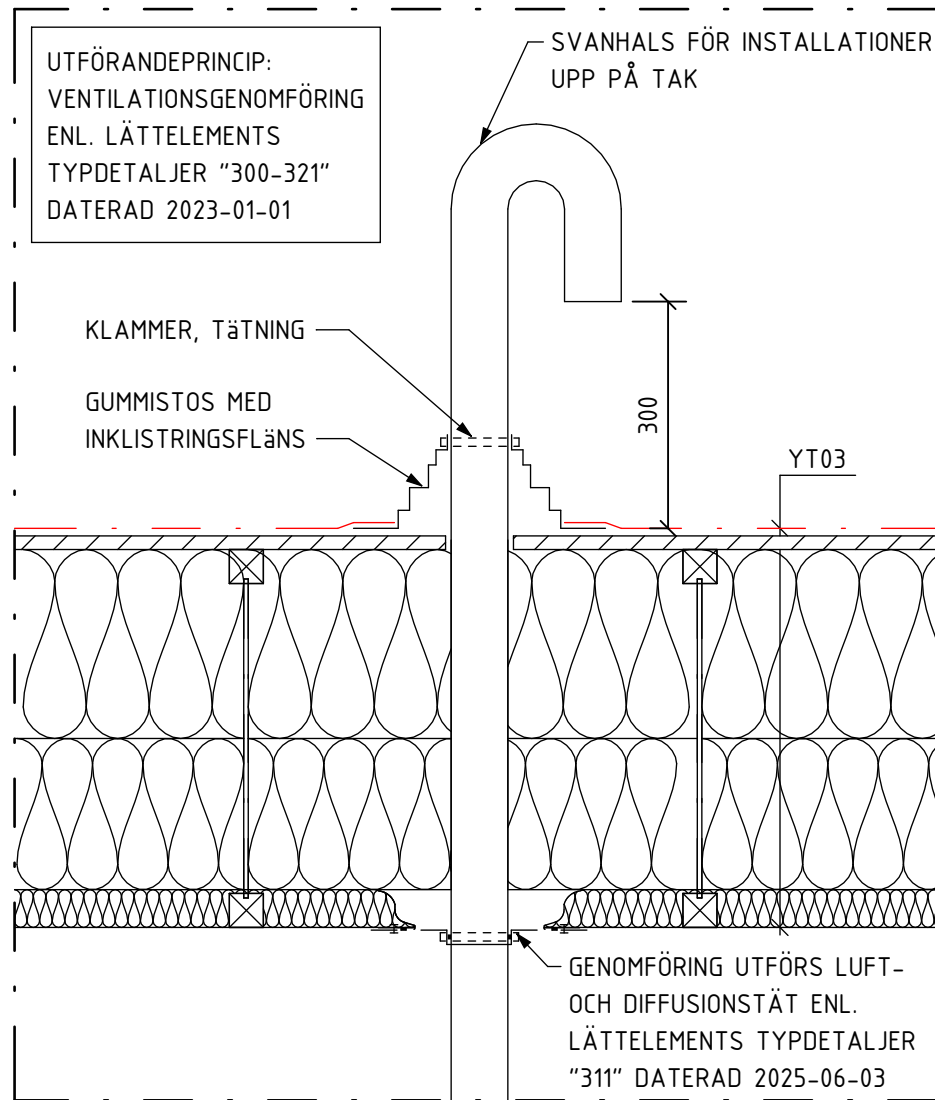

PRINCIPDETALJ 1:10

PRINCIPDETALJ SVANHALS -
RÖRUPPSTICK INSTALLATIONER PÅ TAK
TAK I VAGNHallen MED LJUDREDUKTION

SKALA 1:10

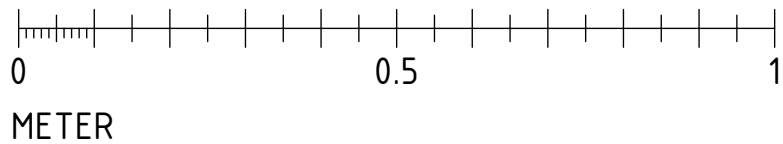

FÖRKLARINGAR

YT= YTTERTAK
YVB = YTTERVÄGG BÄRANDE

SP= STÅLPELARE

FÖRESKRIFTER

SE RITNING

K-00-0-000x-447001

HÄNVISNINGAR

FÖRESKRIFTER
VÄGG- & BJÄLKLAGSTYPER
TAKPLANER
TAKTYPER

K-00-0-000x-447001
K-20-6-0020-447001
K-41-1-0300-447001
K-41-6-0040-447001

SEKTION			
ORIENTERINGSFIGUR			
STATUS			
GODKÄND			
HANDLING			
BYGGHANDLING			
DATUM			
2025-12-12			
SIGNERAD AV			
ANDERS HEDBERG			
BESTÄLLARE			
TIERPS KOMMUNFASTIGHETER			
PROJEKTNAMN			
SÖDERFORS BRANDSTATION			
CARA			
TIERP SÖDERFORS			
PROJEKTNUMMER			
22447001			
ADRESS			
TIERPSVÄGEN			
SHARNUMMER			
JÖRSON 9:4			
DISCIPLIN			
K			
FÖRETAG			
KÄVER OCH MELLIN AB			
UPPDRAGSRUMMER			
24370			
KONTAKTPERSON			
SOFIA THURESSON			
TELEFON			
073-330 87 06			
BYGGNADSVECK			
ANDERS HEDBERG			
BYGGNADSVECK			
PLÅNID (BY 2008)			
VÄNINGSPLAN			
VÄNINGSDEL			
DELOMRÅDE			
SYSTEM			
41-YTTERTAK			
SPECIFIKATION			
TAKDETALJER			
DETALJ			
SKALA			
1:5, 1:10			
FORMAT			
A1			
DOKUMENTNUMMER			
K-41-6-0042-447001			
ÄNDRING			